

HASSAN M SHATA
Architectural Portfolio.
Selected Works

PROFESSIONAL WORK

2604 Sevier st <i>Durham,NC</i>	4
Salem Cohousing <i>Winston Salem,NC</i>	6
11 Fox Run <i>Westerly, RI</i>	10
Rey Cement Factory - Competition <i>Tehran, Iran</i>	16
Atlantic Beach Public Safety & Admin Complex <i>Atlantic Beach, NC</i>	18


“The Sun does not realise how wonderful it is until after a room is made.”
- Louis Kahn

SCHOOL WORK


Community Center-St Agnes <i>Raleigh, NC</i>	24
Visitor Center <i>Eagles Island, NC</i>	26
New Bern Public Library <i>New Bern, NC</i>	34

2604 Sevier Street


This project involved adding a new sunroom and extending the primary bedroom by removing a secondary bedroom. After exploring various schemes, the clients selected the most sustainable and comfortable solution. We maximized the available space while ensuring minimal structural changes. Frequent meetings allowed us to align the plan with the clients' specific goals.

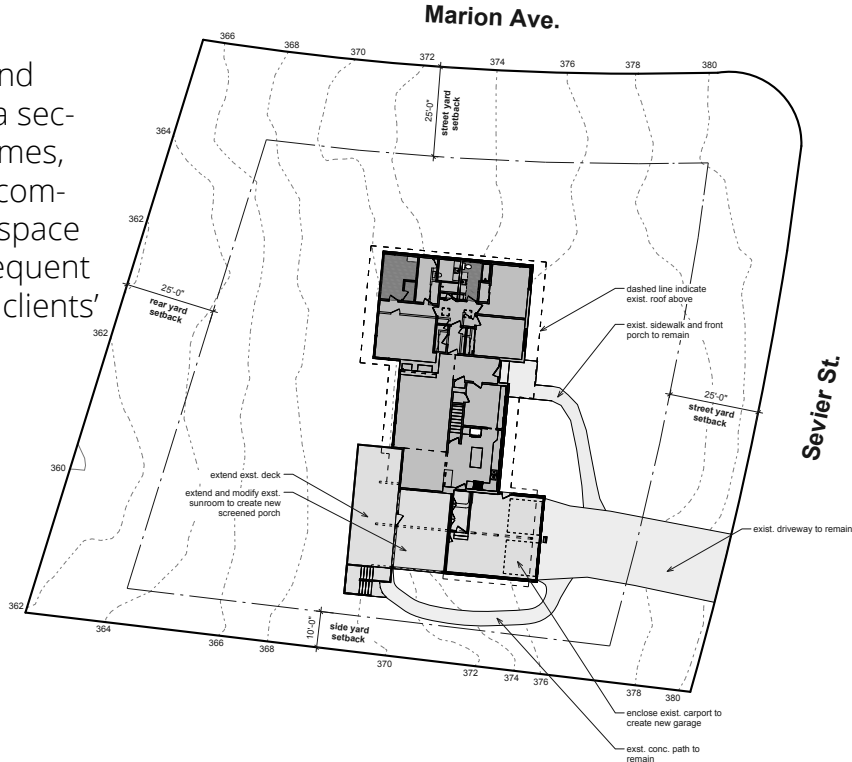


Site Plan

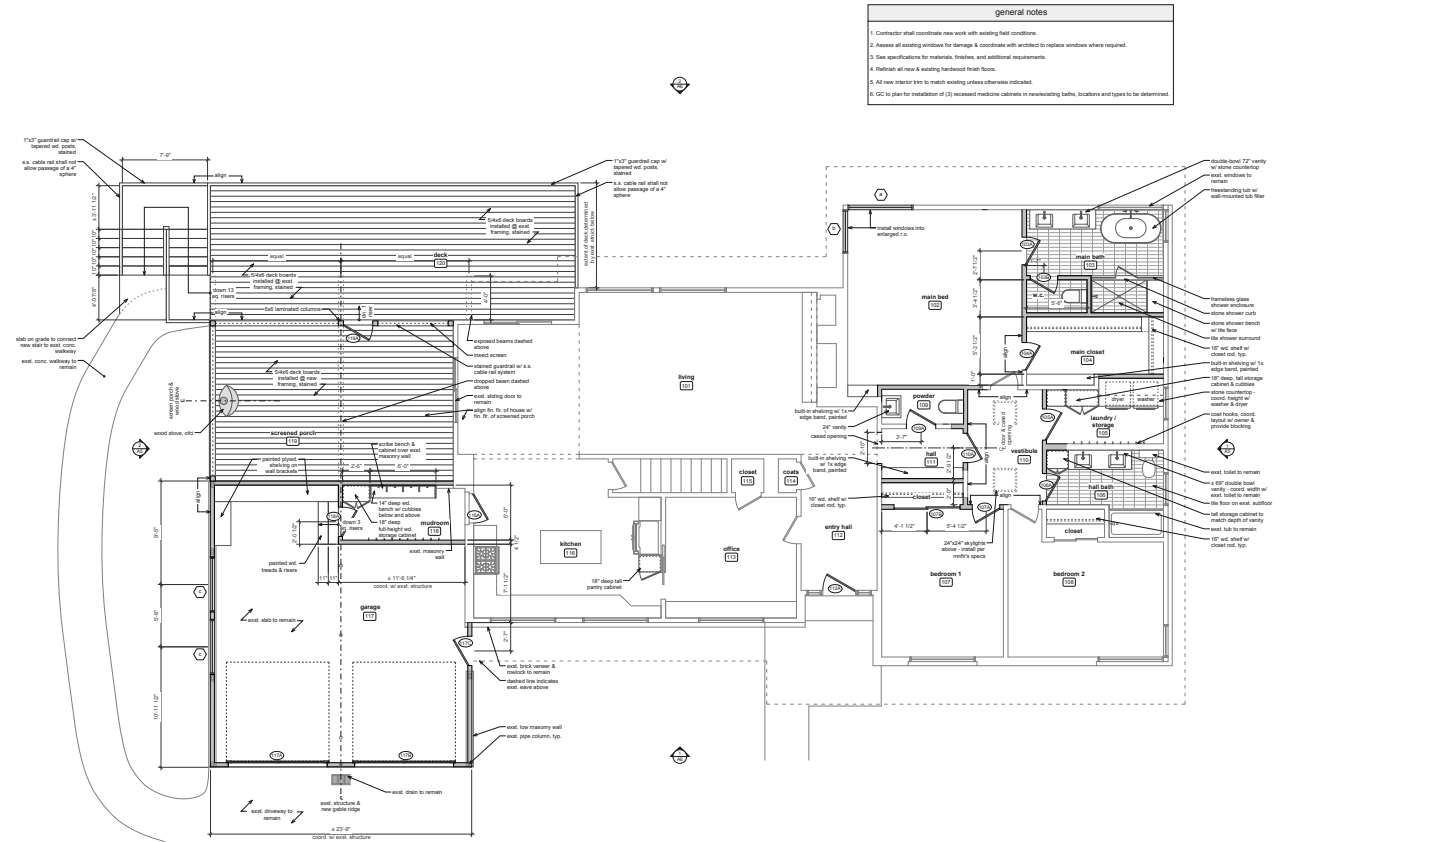


Floor Plan

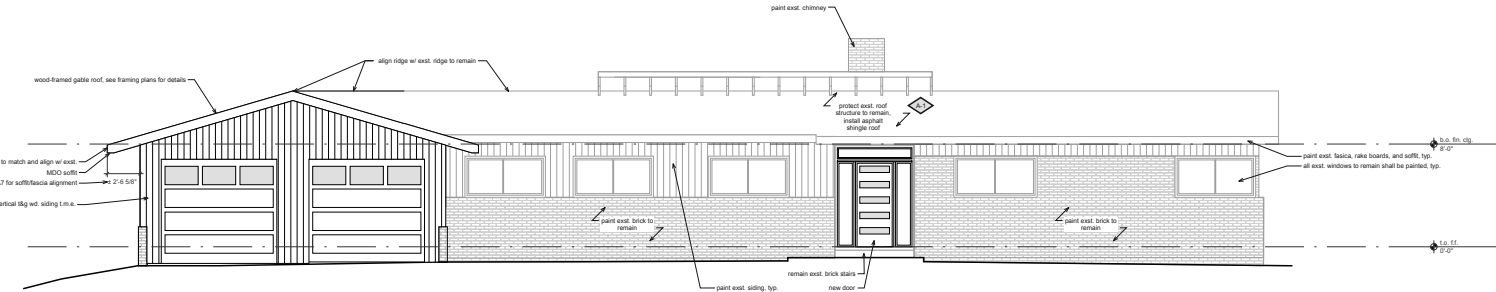


East Elevation

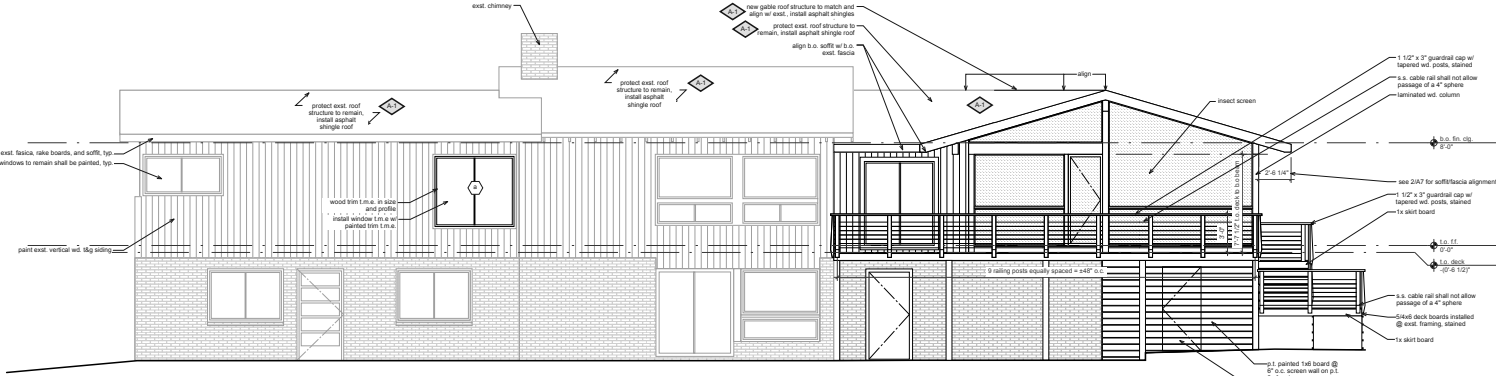

West Elevation

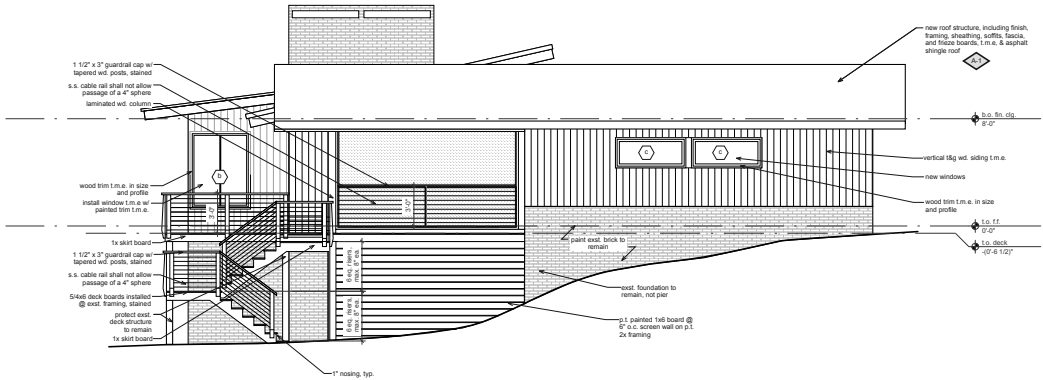

South Elevation

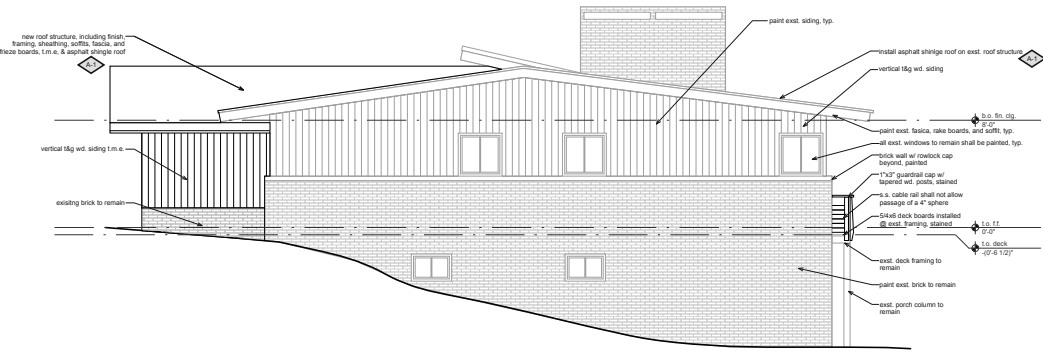

North Elevation


Salem Cohousing

Our team worked with Rasheeda to design the first co-housing building in Winston-Salem. We wanted to create a safe space for single mothers. This community gives them new opportunities and helps reduce their daily stress so they can grow mentally and emotionally. In this shared space, multiple families live together and take part in activities that help them thrive. This project, Salem-Cohousing, is the first communal living model of its kind in the city.



plan ground floor

- | | |
|-----------------------|----|
| Utility Room | 1 |
| Office | 2 |
| Storage | 3 |
| Library/Workspace | 4 |
| Powder Room | 5 |
| Yoga/Cardio/Playspace | 6 |
| Elevator | 7 |
| Indoor Staircase | 8 |
| Therapy | 9 |
| Bedrooms | 10 |
| Bathrooms | 11 |
| Laundry Room | 12 |
| Kitchen | 13 |
| Living Space | 14 |
| Outdoor Garden | 15 |

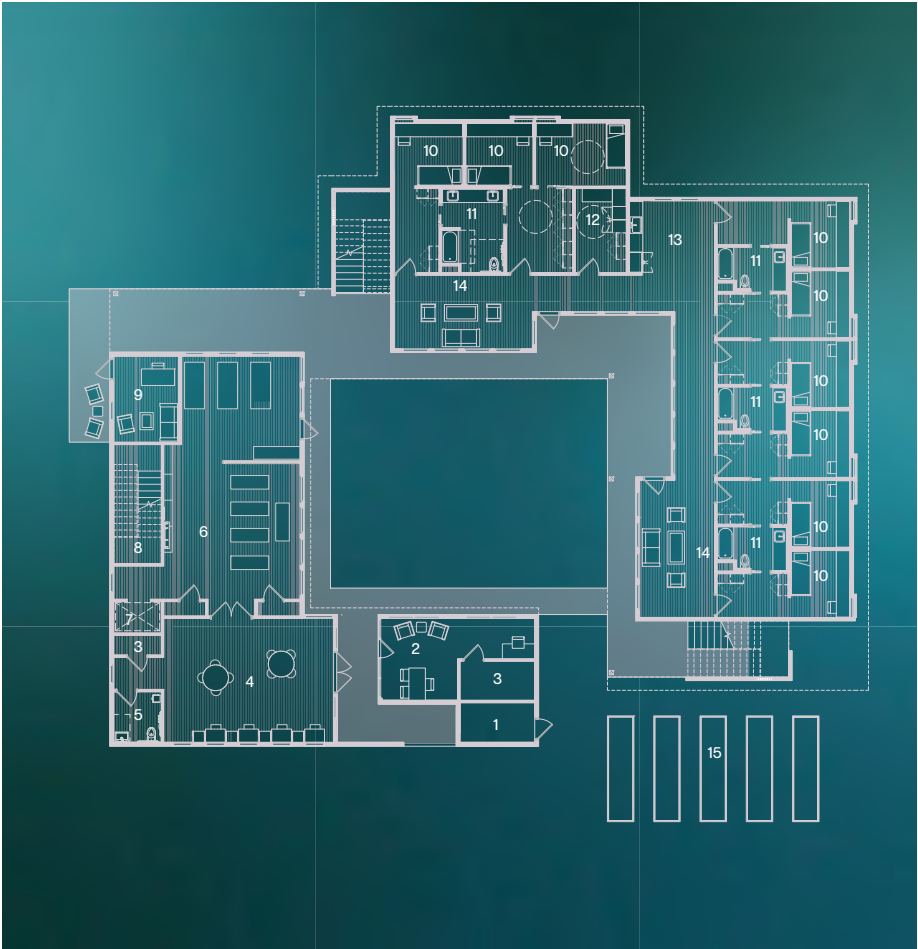

plan second floor

- | | |
|---------------------|----|
| Indoor Staircase | 1 |
| Elevator | 2 |
| Storage | 3 |
| Powder Room | 4 |
| Dining | 5 |
| Living | 6 |
| Kitchen | 7 |
| Pantry | 8 |
| Herb Garden/Balcony | 9 |
| Bedrooms | 10 |
| Bathrooms | 11 |
| Laundry Room | 12 |
| House Mom's Suite | 13 |





Interior View




Exterior View




11 FOX RUN


This project involves the design of a 5,150-square-foot house located in Westerly, RI. The design evolved from a single large mass into a composition of several smaller masses, each representing a different program. I worked on this project during the schematic design phase. My primary responsibilities included testing forms through physical and digital models, collaborating on presentation drawings in Illustrator, and developing the exterior renderings.

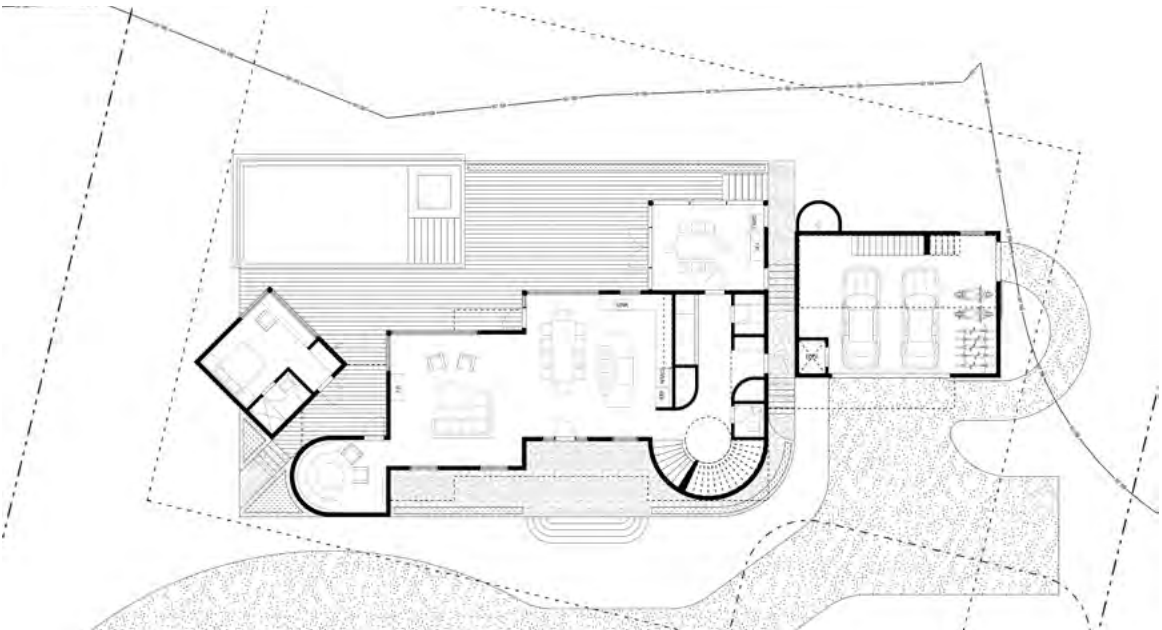


First Floor

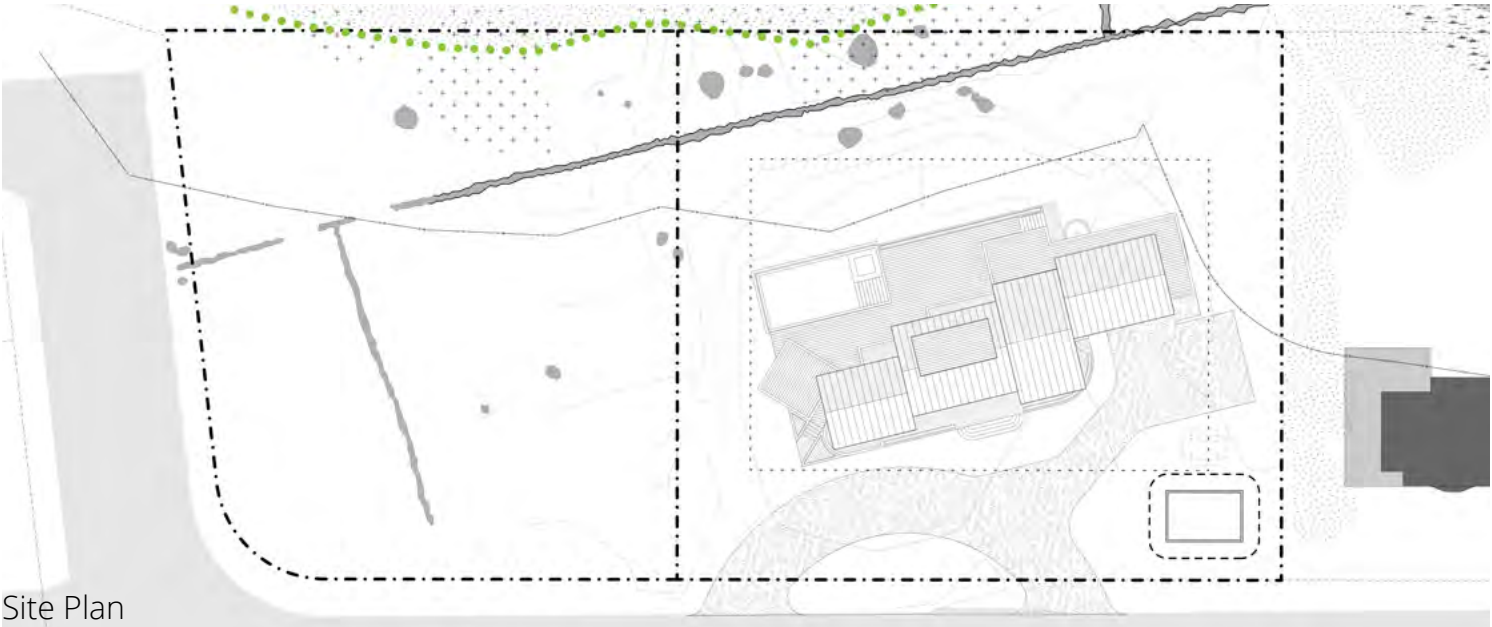


Site Plan

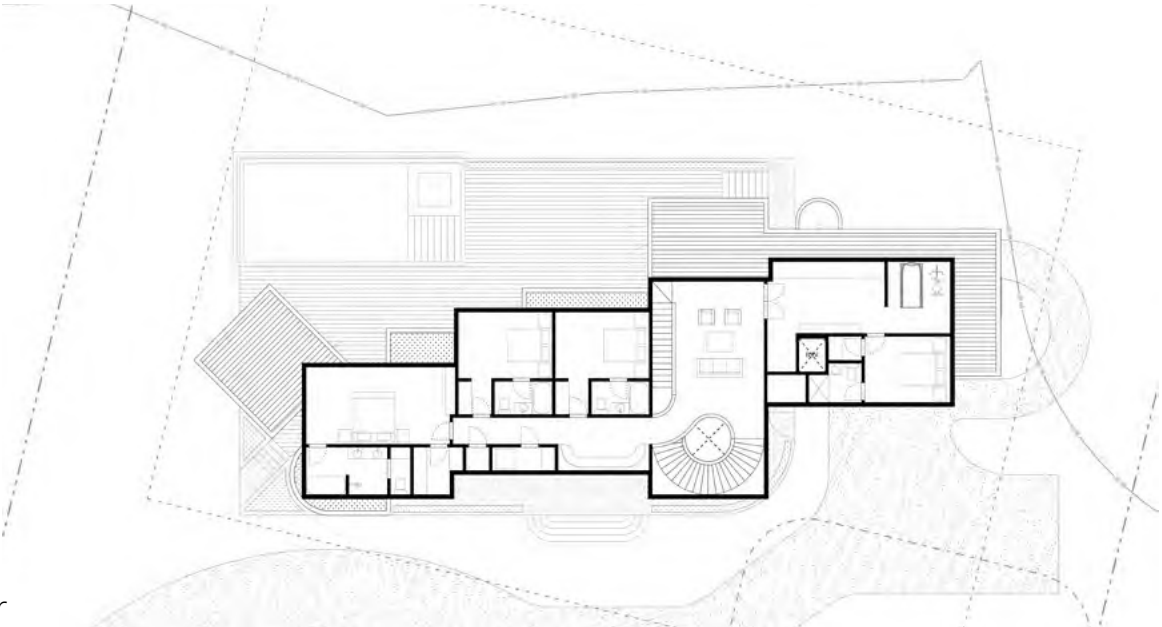


Second Floor

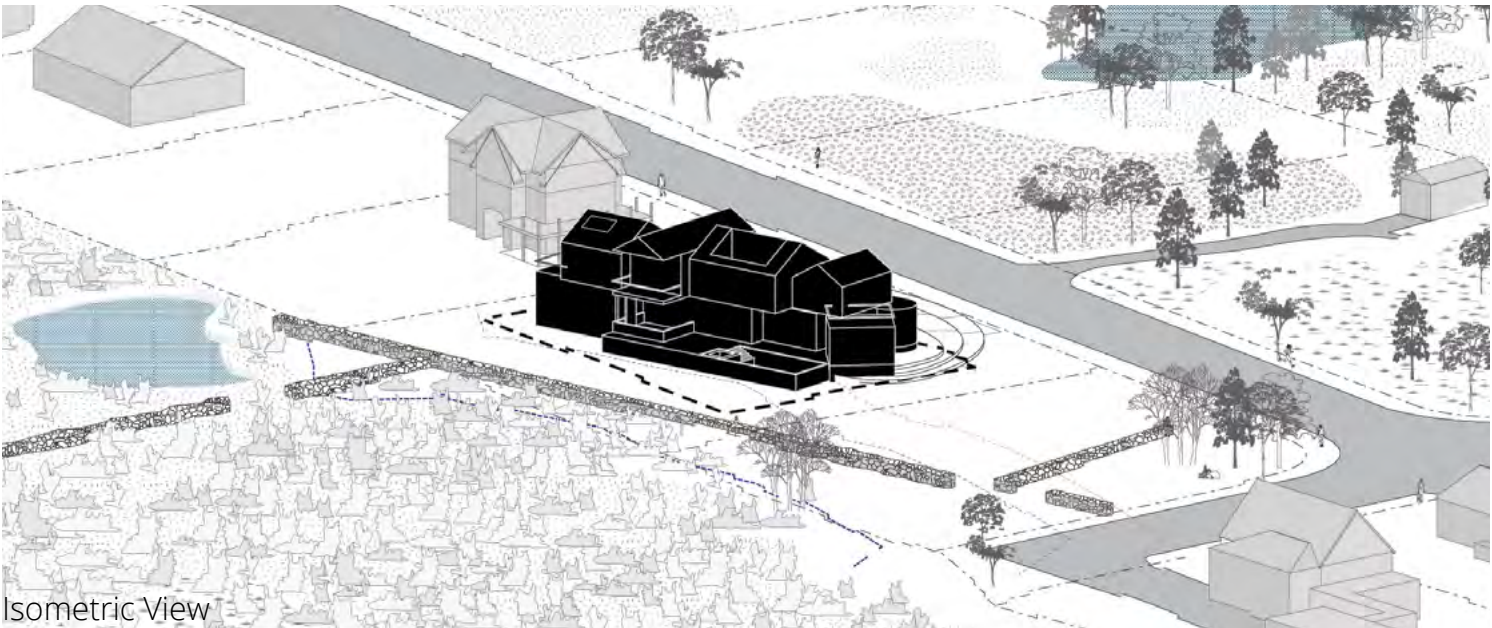

Isometric View

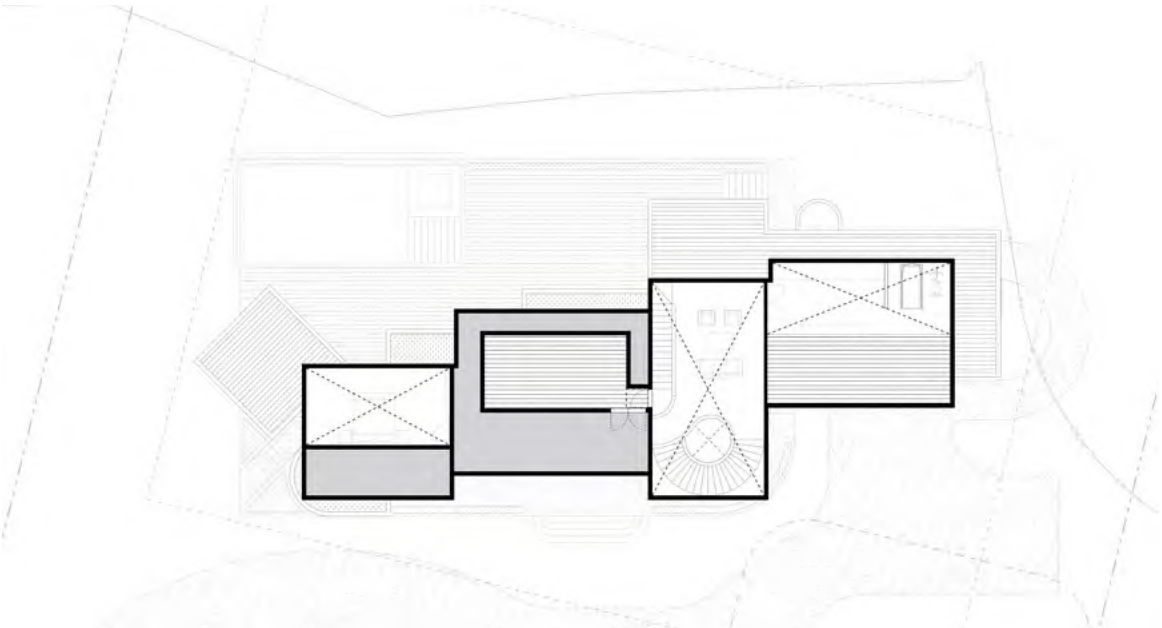

Third Floor

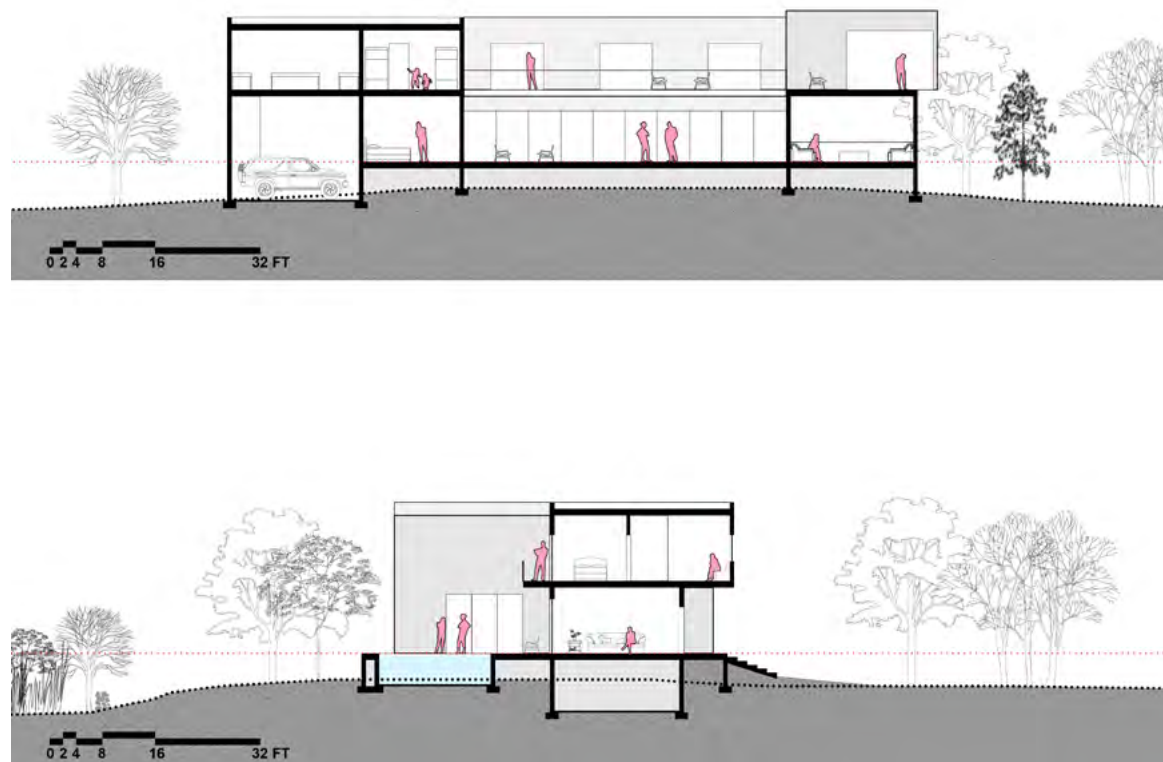


Sections




Rey Cement Factory

The Rey Cement Factory is located in the south-eastern quadrant of Tehran, Iran. This project involves the adaptive reuse of a former industrial complex once used for concrete production. As a significant example of Iran's industrial heritage, our strategy is to activate the site by introducing new programs and activities.


Our proposal introduces over 90,000 m² of educational, recreational, cultural, and religious programming. We added a new structure to connect and frame these programs, creating an elevated ground plane that floats above the city.

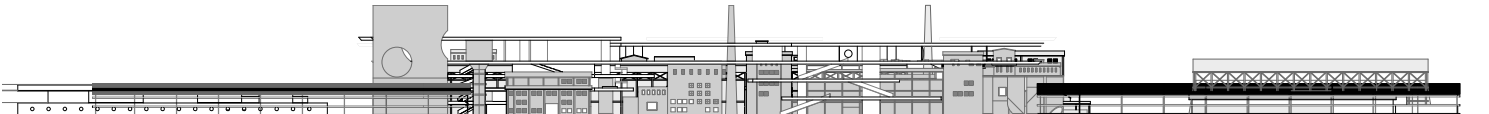


South Elevation

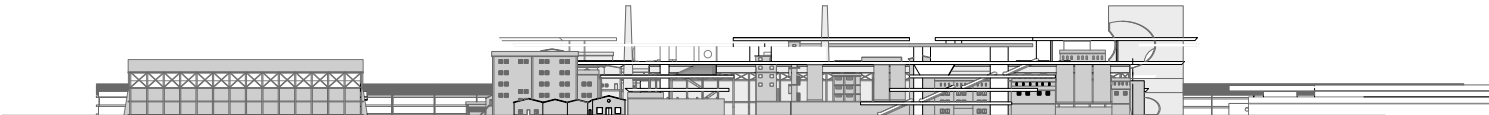



North Elevation


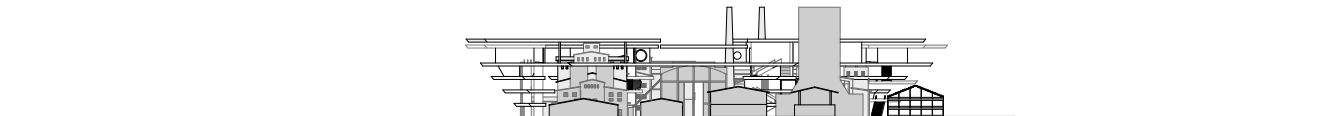


West Elevation

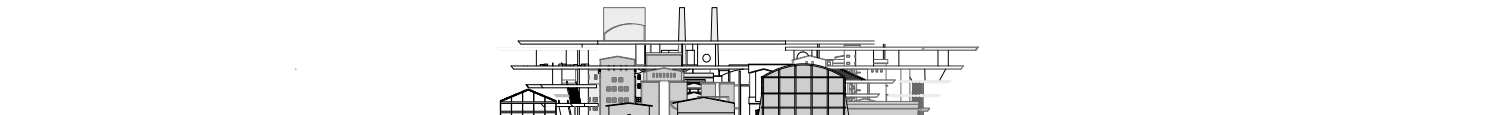

East Elevation

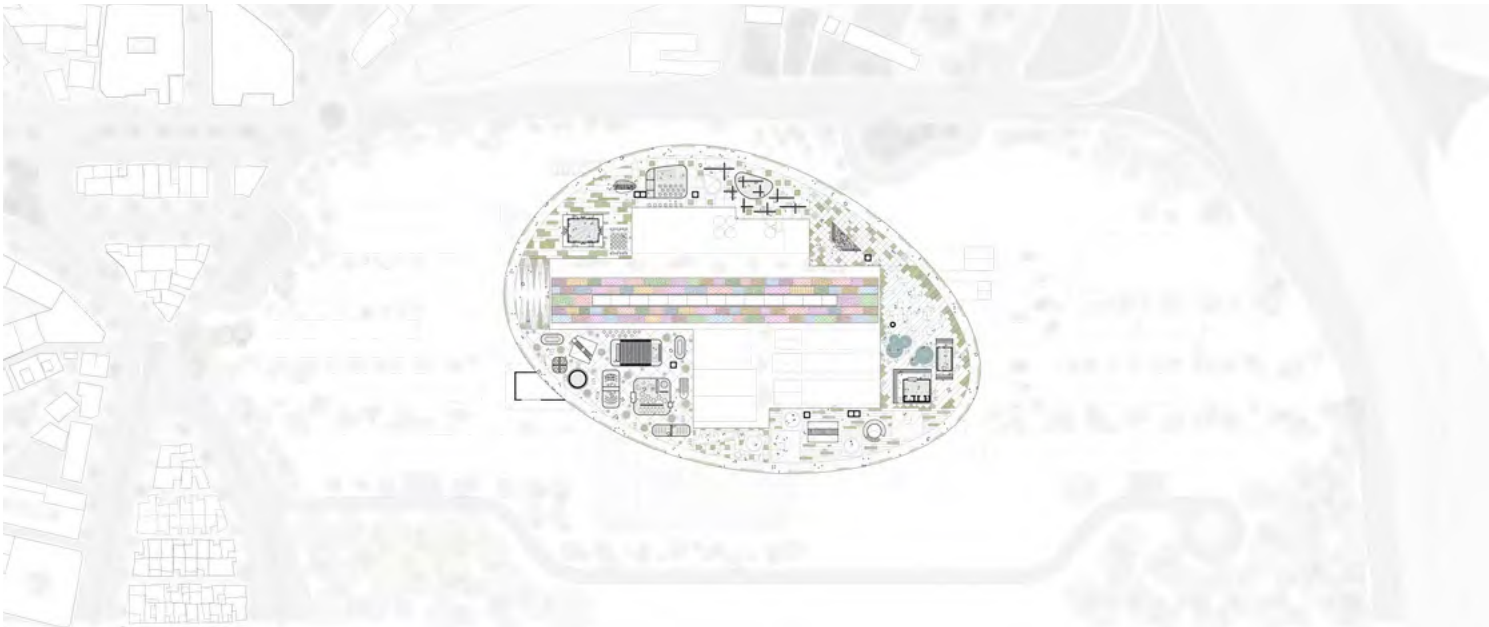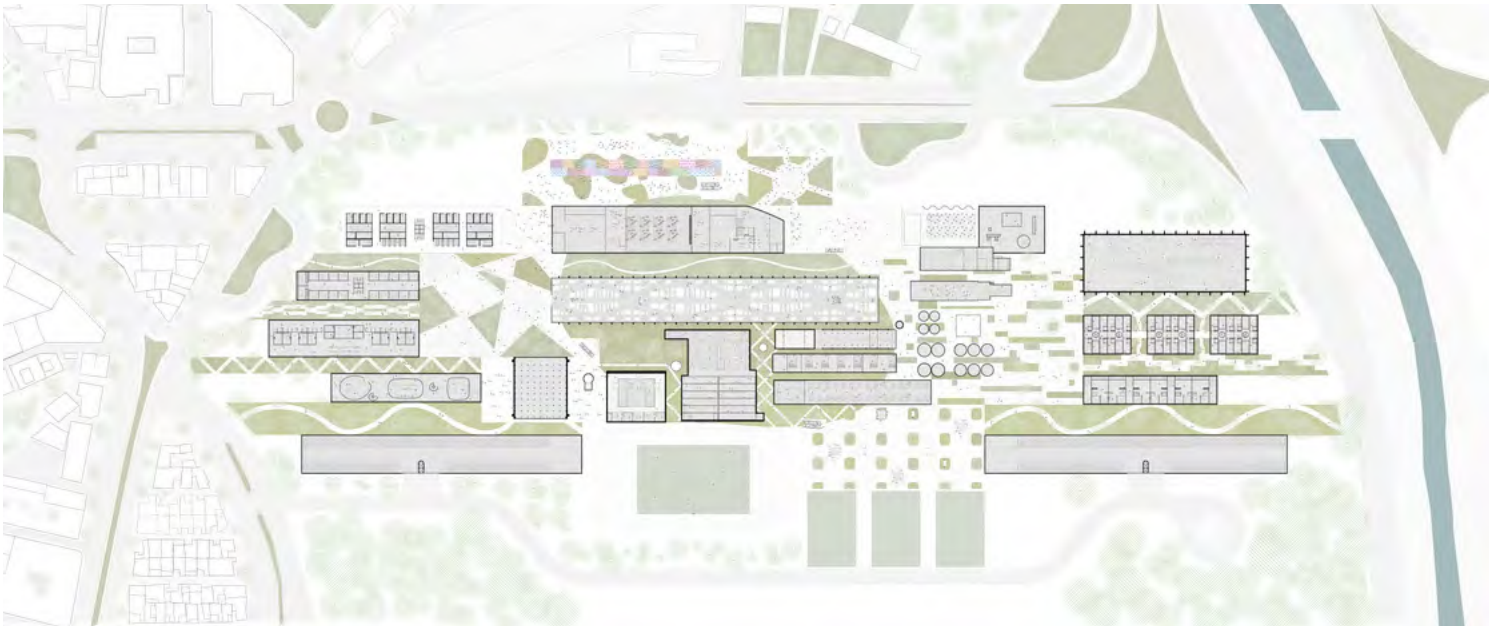


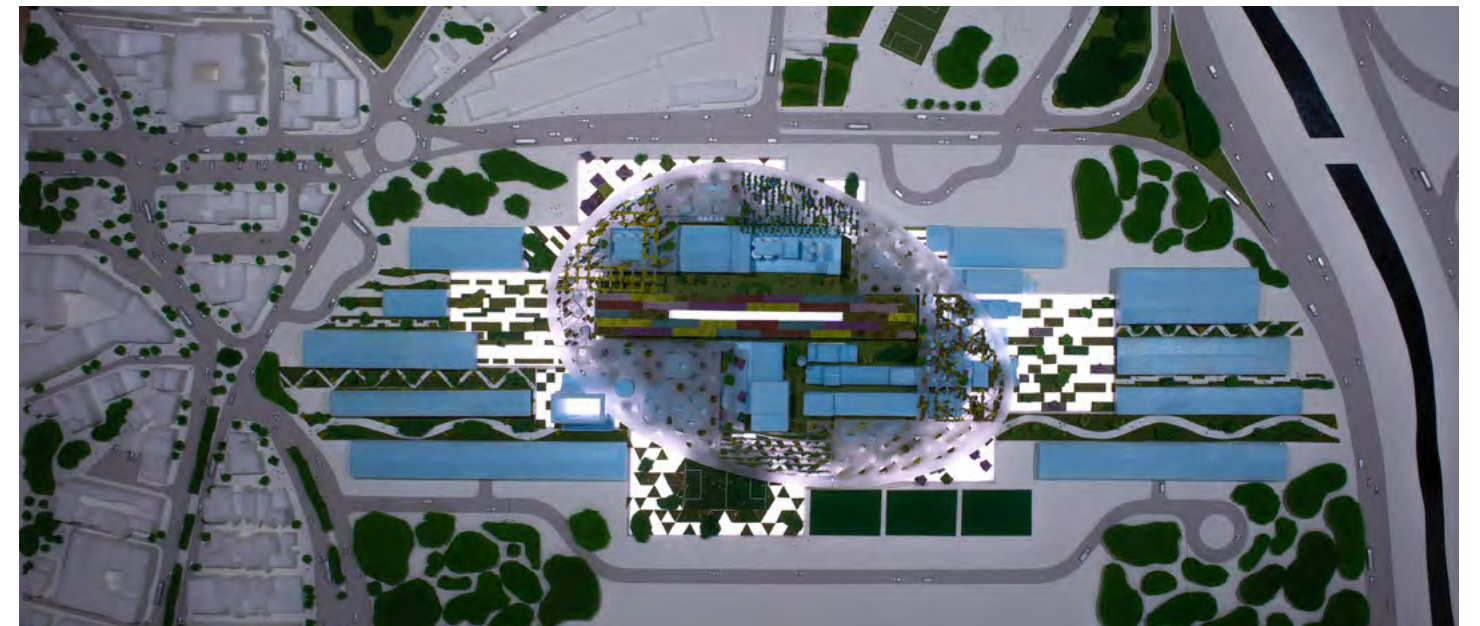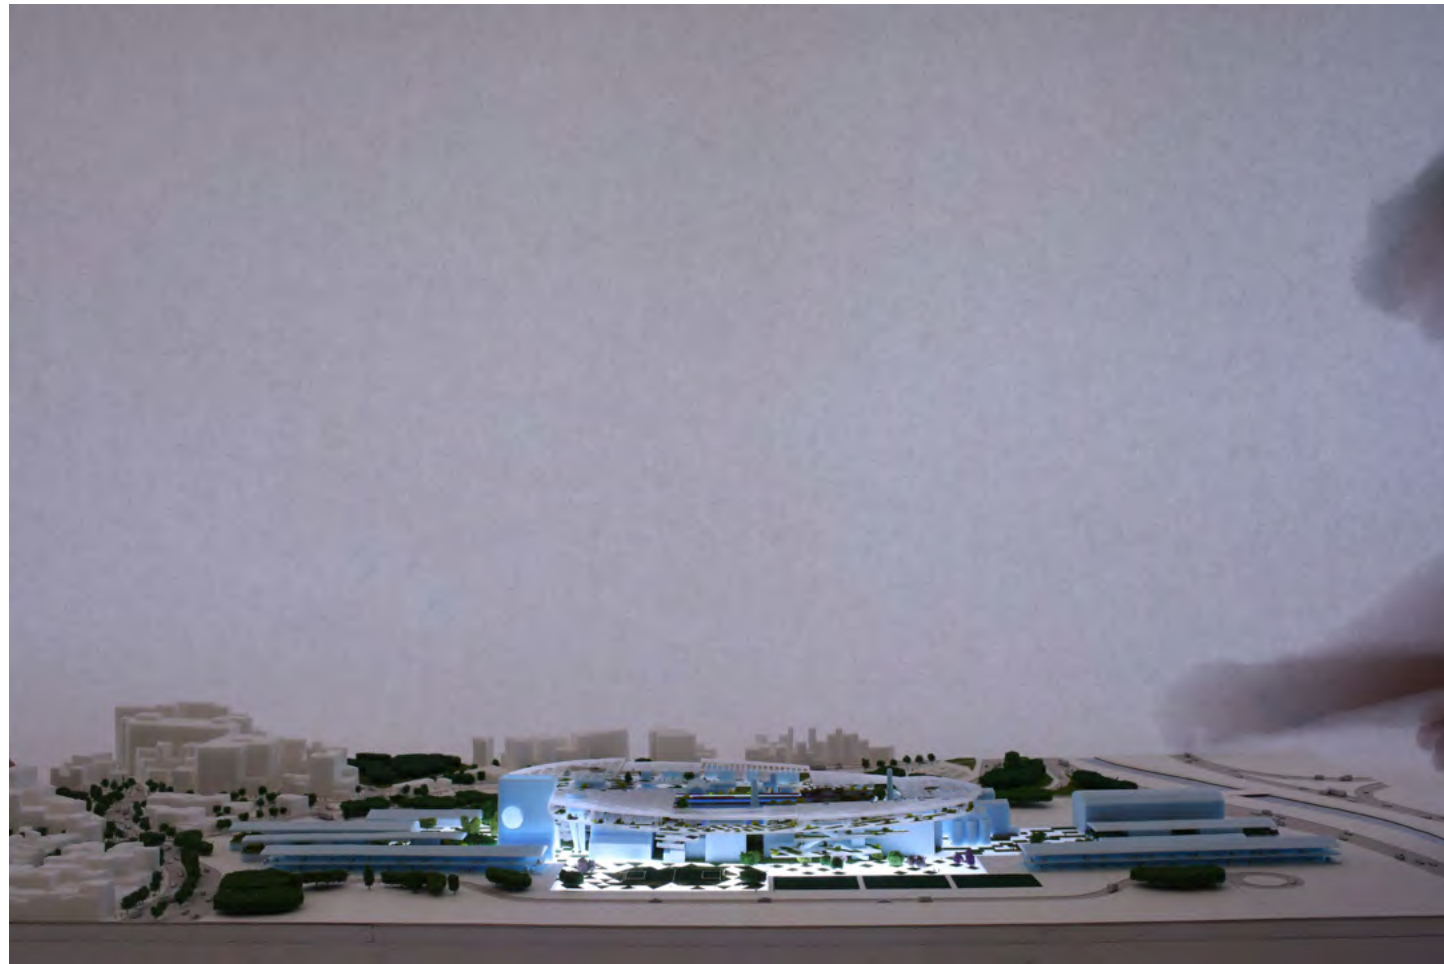


Atlantic Beach Public Safety & Admin Complex

This project involves the new Public Safety and Administrative Complex for the town of Atlantic Beach, North Carolina. The program includes a new Town Hall, administrative offices, a police station, and a fire department. The project totals 20,150 square feet and will be constructed in two phases. Conceptually, we focused on breaking down the scale of the massing to reflect the residential neighborhood to the south.


I contributed to this project from Schematic Design through Construction Documents. My primary responsibilities included testing forms through physical and digital models, as well as creating presentation drawings in Illustrator and developing the exterior renderings.

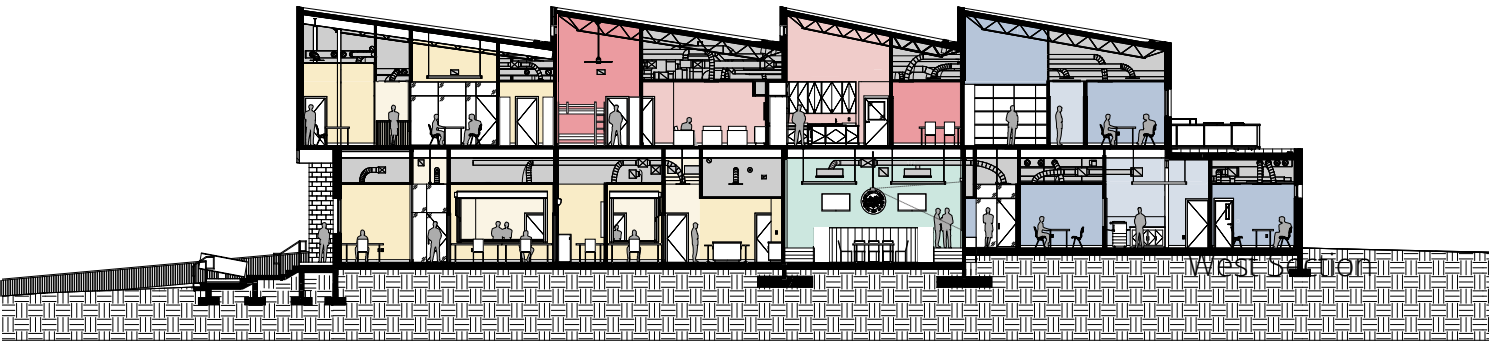

West Section

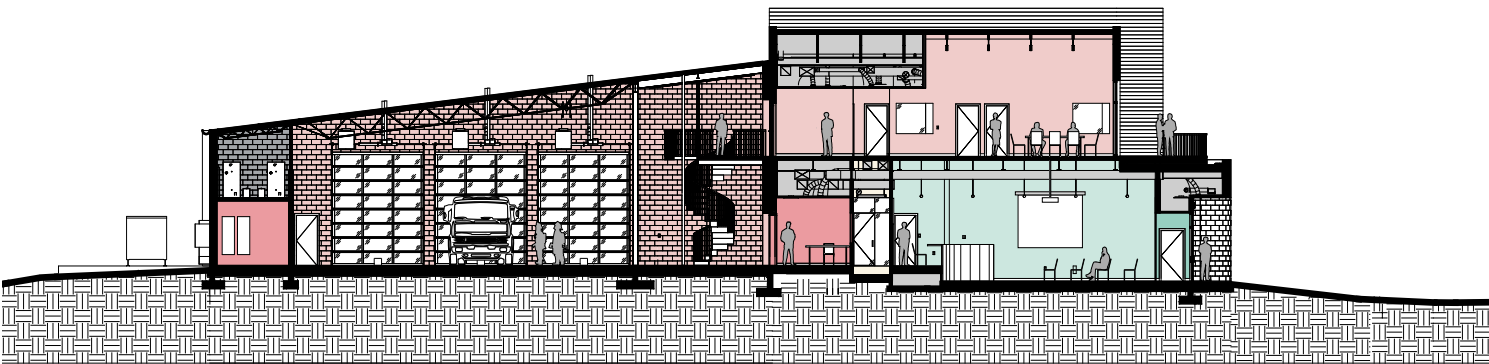

North Section

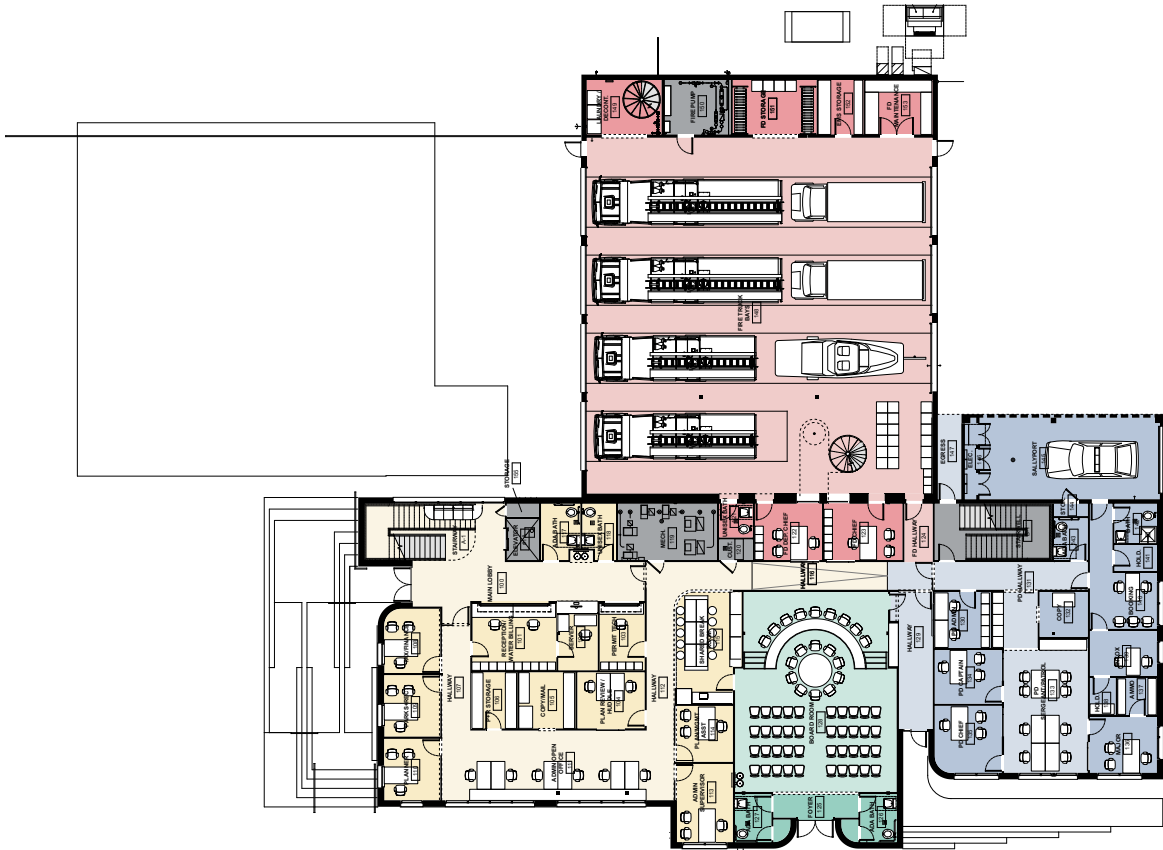

First Floor



Second Floor





Community Center-St Agnes



Activating and transforming the abandoned, historical St. Agnes Hospital at Saint Augustine’s University into a community center, gallery, and restaurant is a commendable goal. This project revitalizes the site while serving both the local community and university students. The process should begin with a thorough historical preservation assessment to ensure the building’s character is retained—specifically by restoring architectural elements, facades, and materials to their original condition. By breathing new life into this site, you can foster deeper connections between the university and its surroundings, creating a vibrant cultural and educational anchor for the area.


<https://vimeo.com/783395129>




Visitor Center

The new visitors center draws inspiration from the historic waterfront warehouses found on the island and throughout the city of Wilmington. Located on the east side of Eagles Island, the building is situated on high ground above the base flood elevation. The design reflects the site's history through an iconic style, creating a strong visual connection with Wilmington's atmosphere. An observation tower was added to provide a unique vertical experience, offering panoramic views of both the city and the island. This tower also provides visual balance and evokes the memory of the smokestacks that once stood near the waterfront. I collaborated on this project with Brian Vaughn, a Master of Landscape Architecture student.

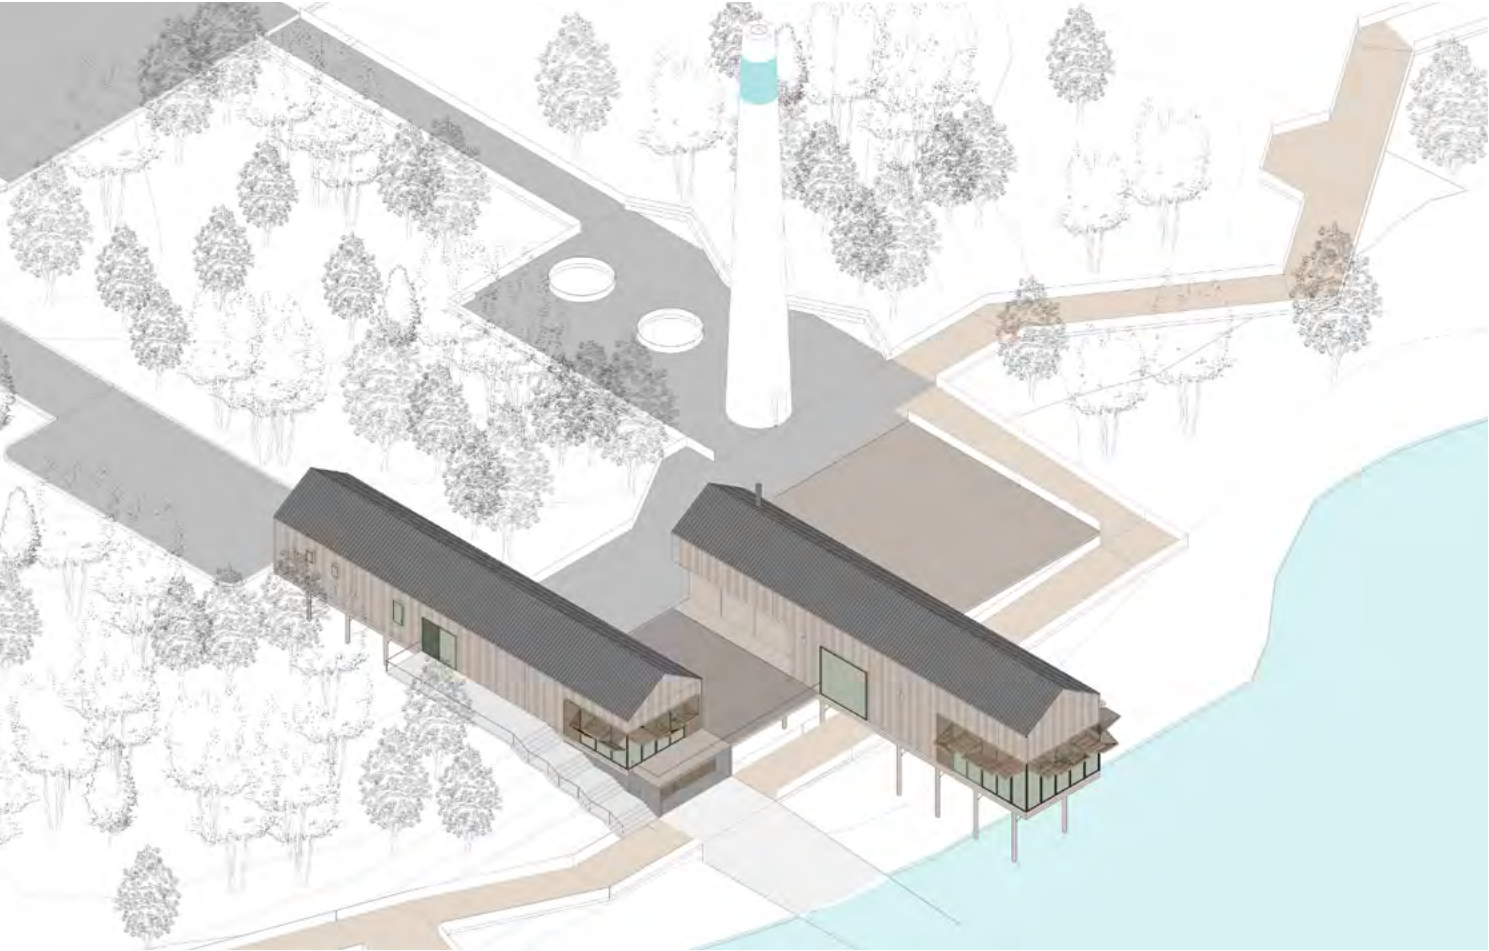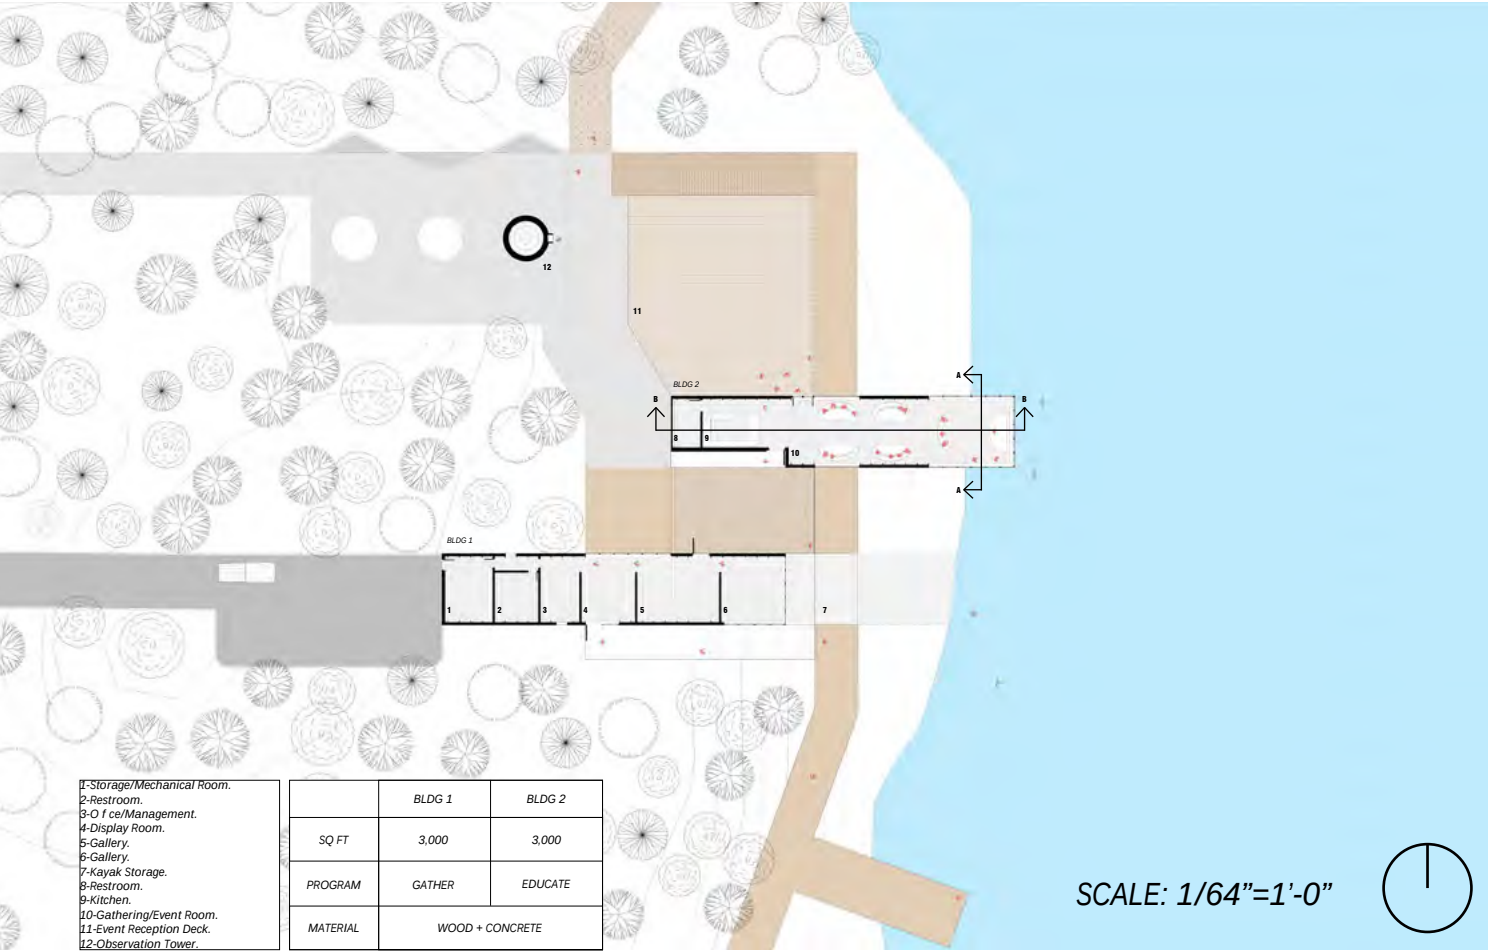


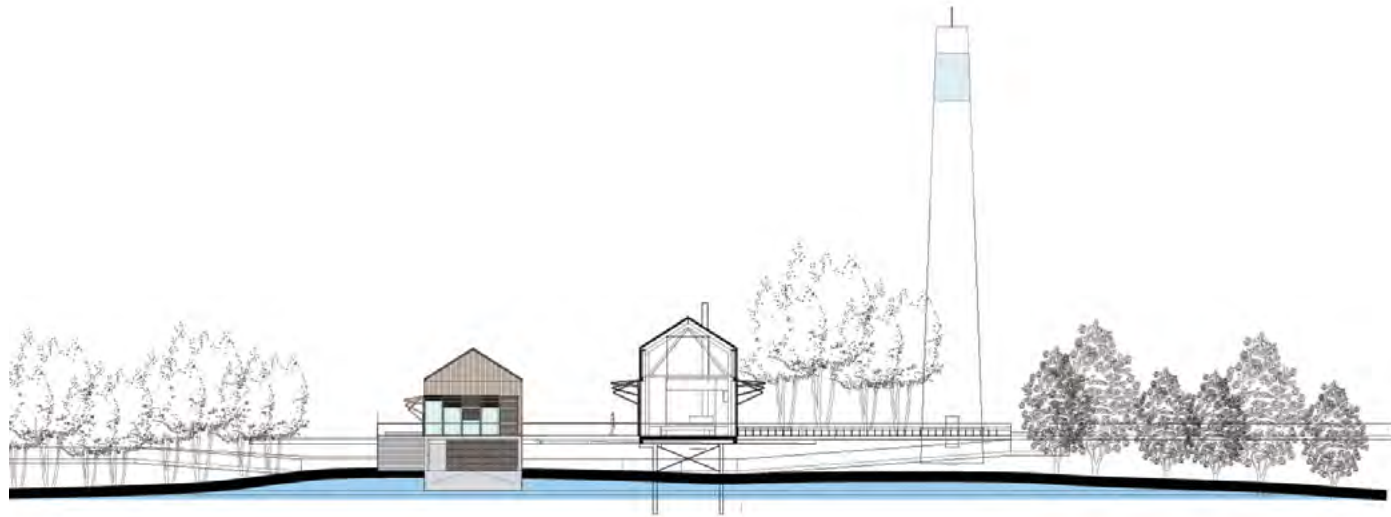

Section A-A

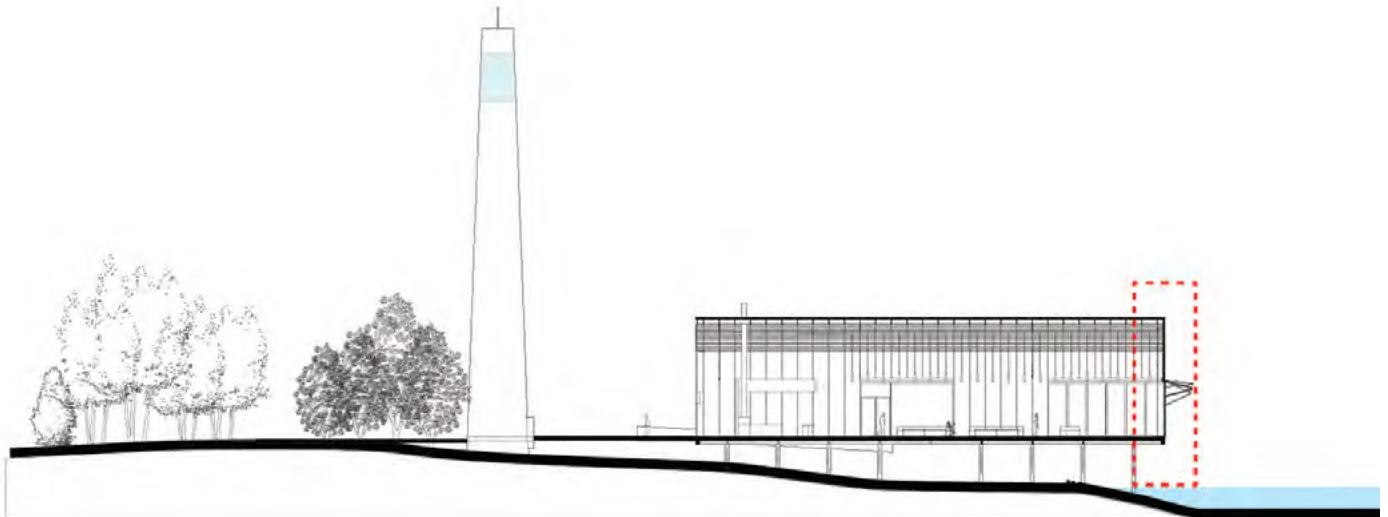


Section B-B

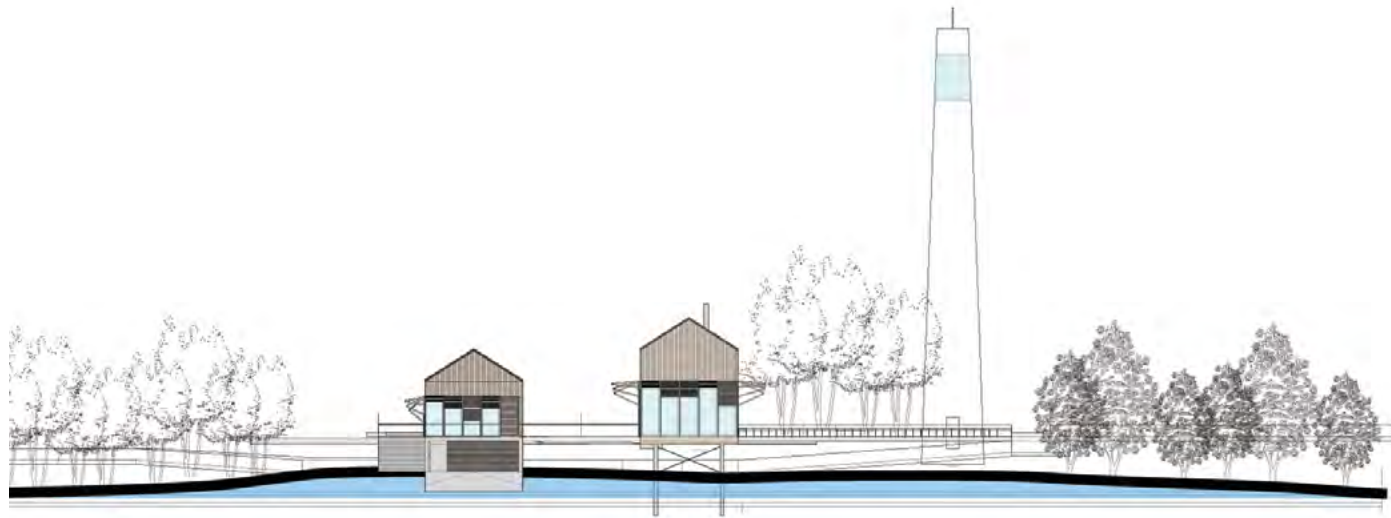

West Elevation



North Elevation

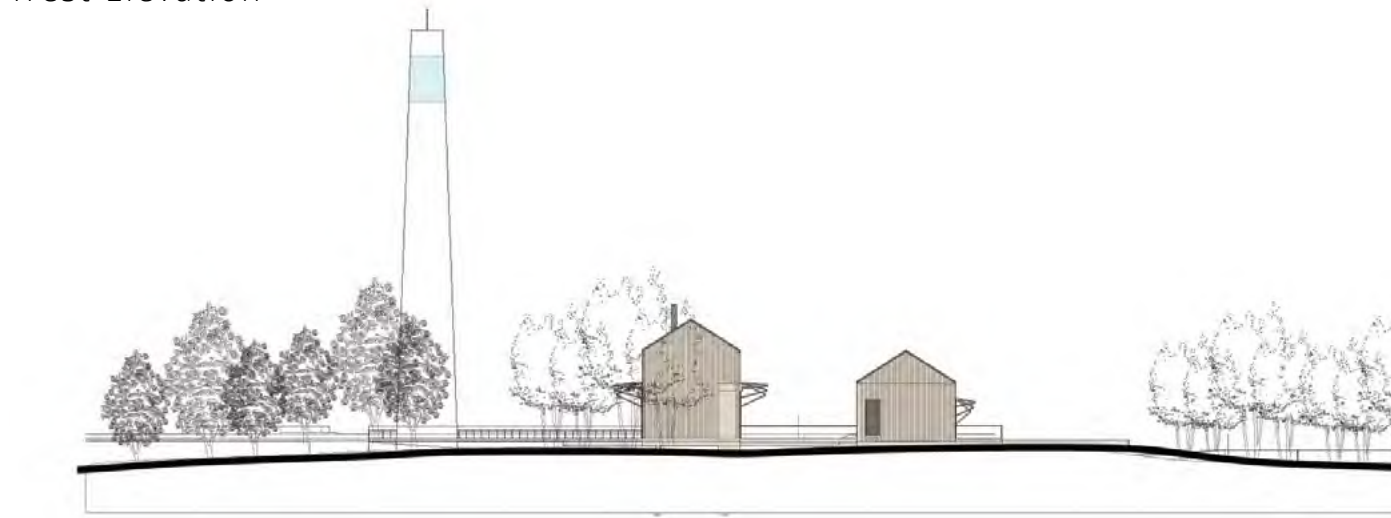


East Elevation




South Elevation



Scale: 1/64"=1'-0"

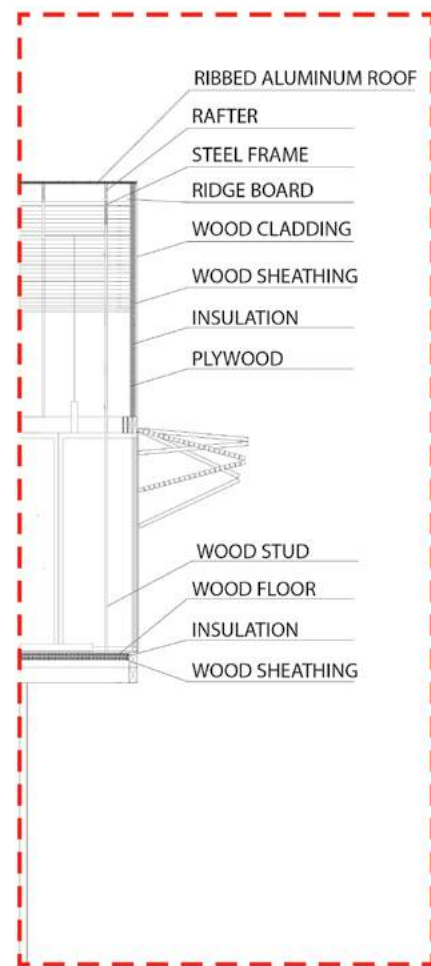

Detailed Section

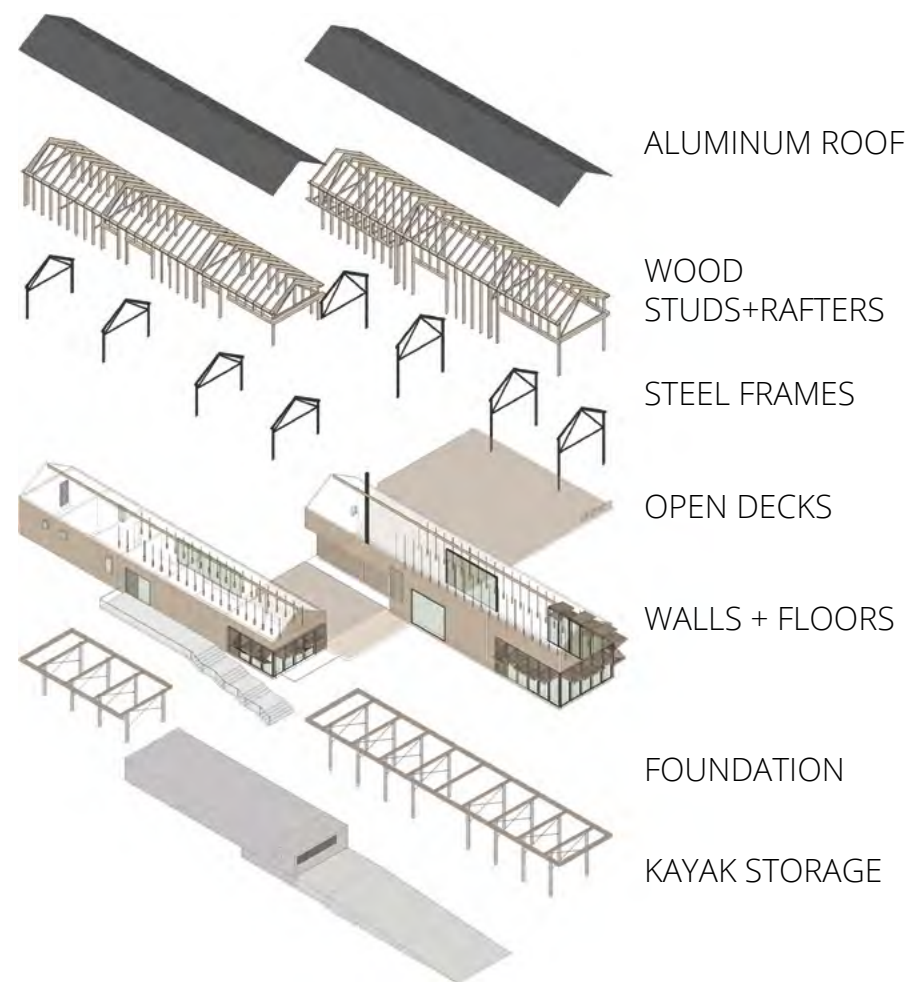




Structural Axon

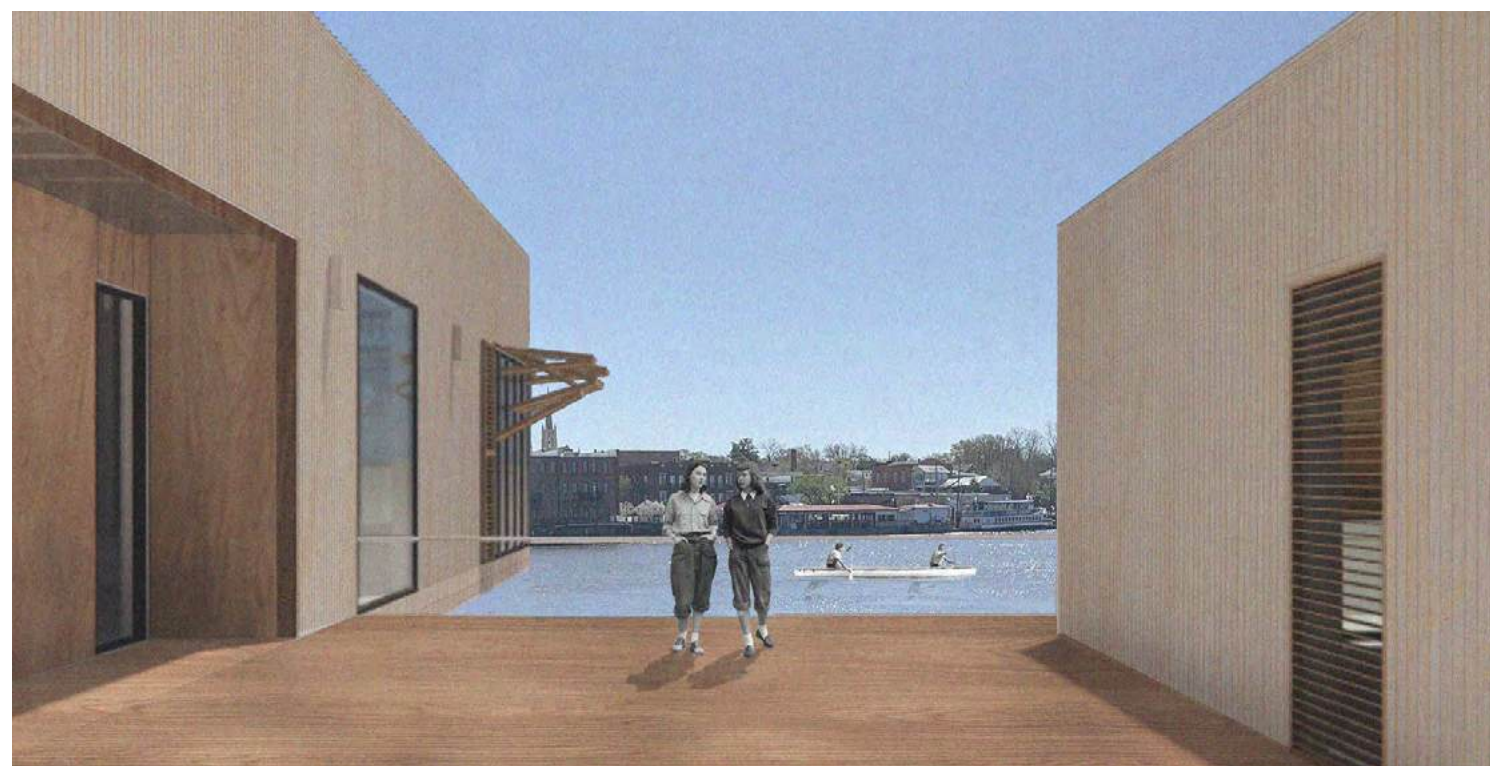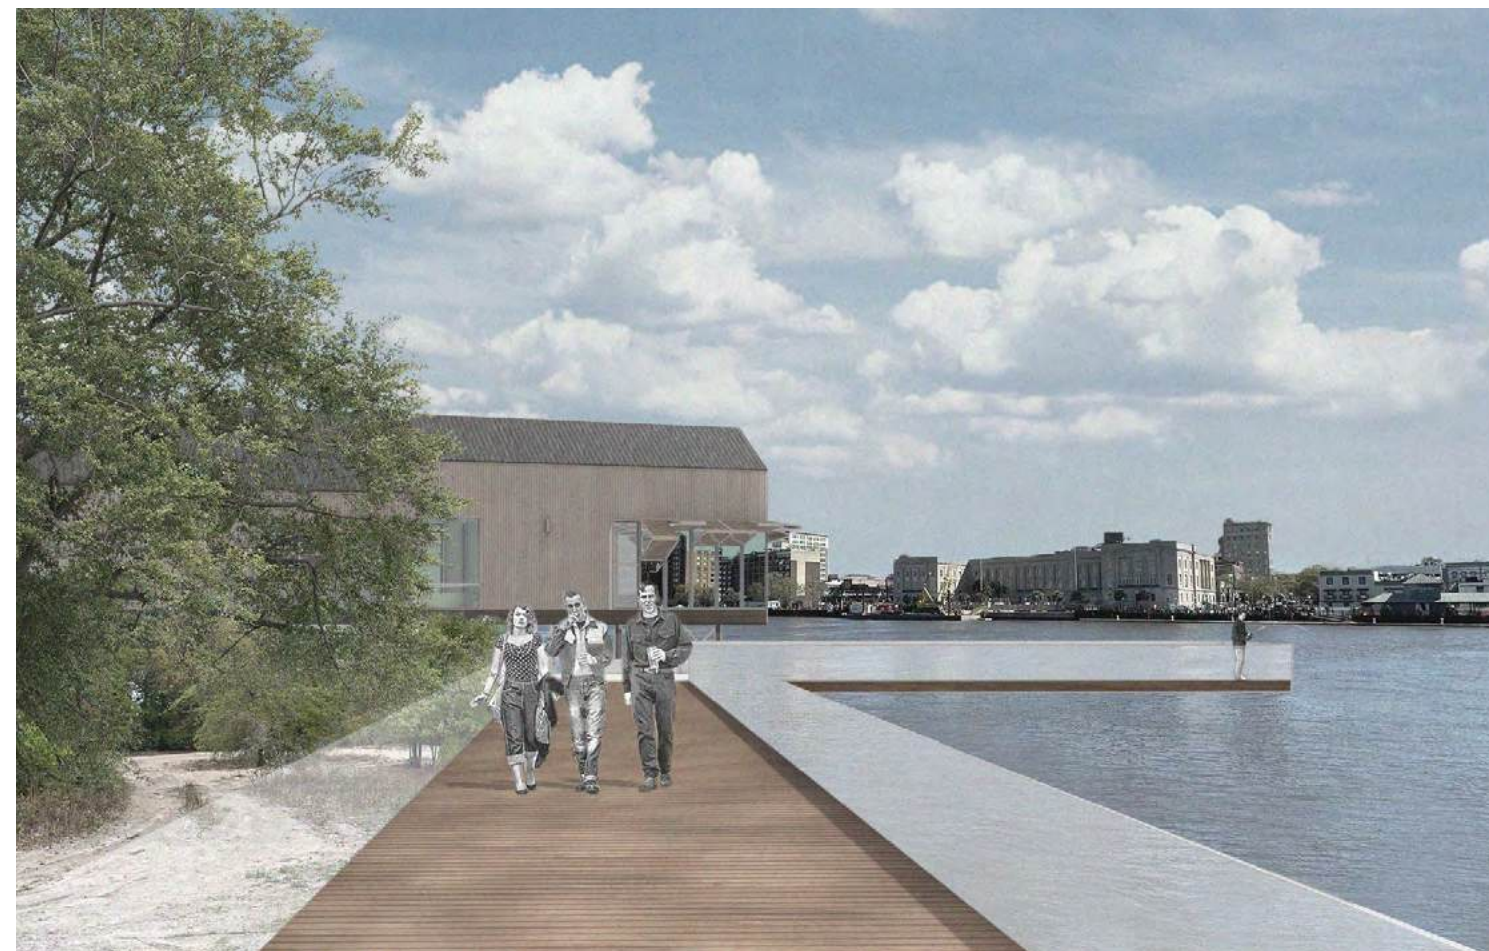




New Bern Public Library


Designing a new library in a historic city like New Bern, North Carolina, presents a unique opportunity to harmonize rich cultural heritage with modern design principles. The goal is to create a civic hub for lifelong learning that fosters interaction and provides comprehensive physical and digital resources. The design prioritizes universal accessibility, incorporating seamless ramps, elevators, and inclusive features for all residents. By maximizing natural light through large glazing and skylights, the library will strengthen the connection between the interior and the outdoors, specifically framing views of New Bern's historic landmarks and coastal landscape

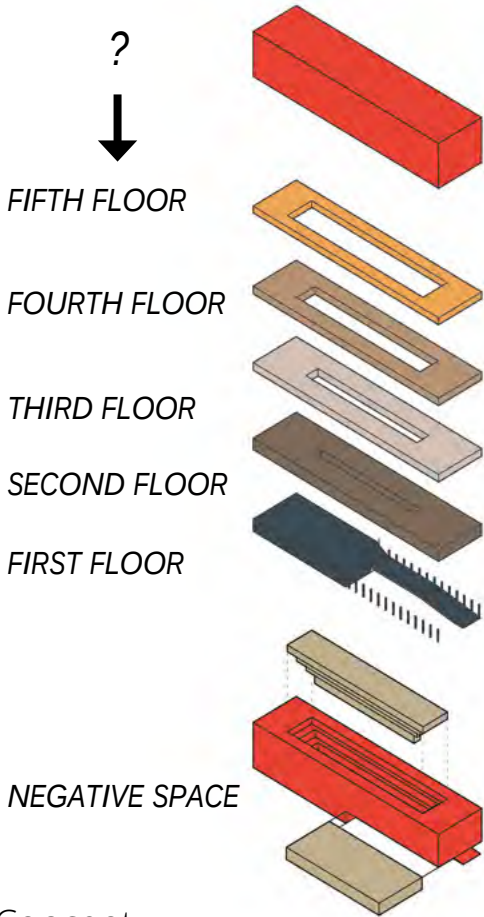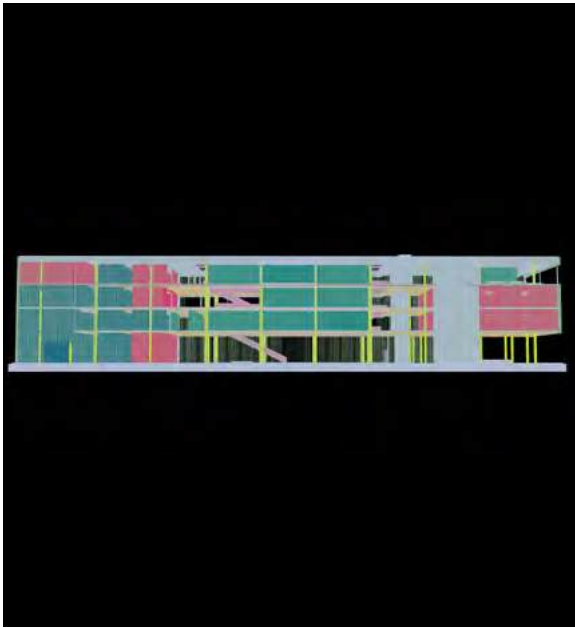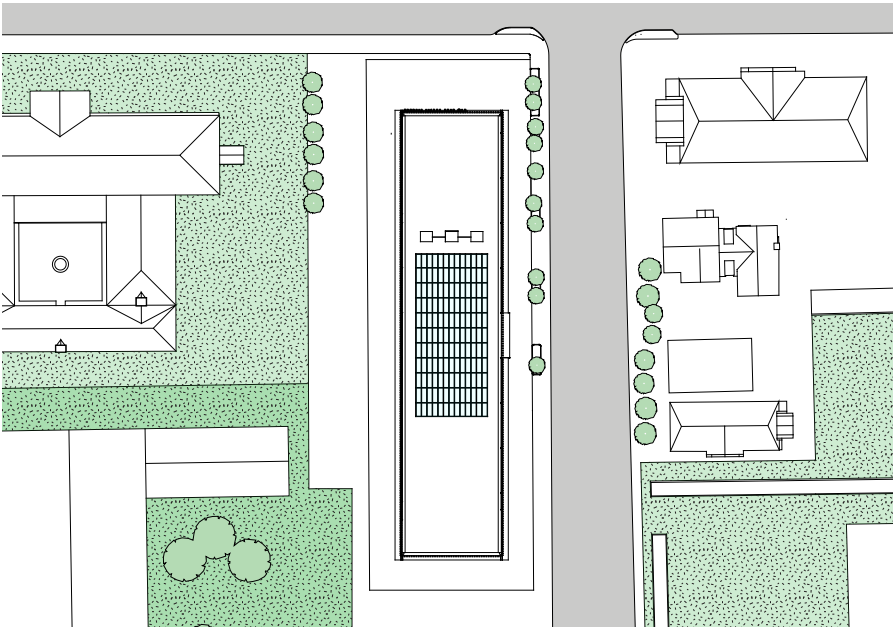


Concept

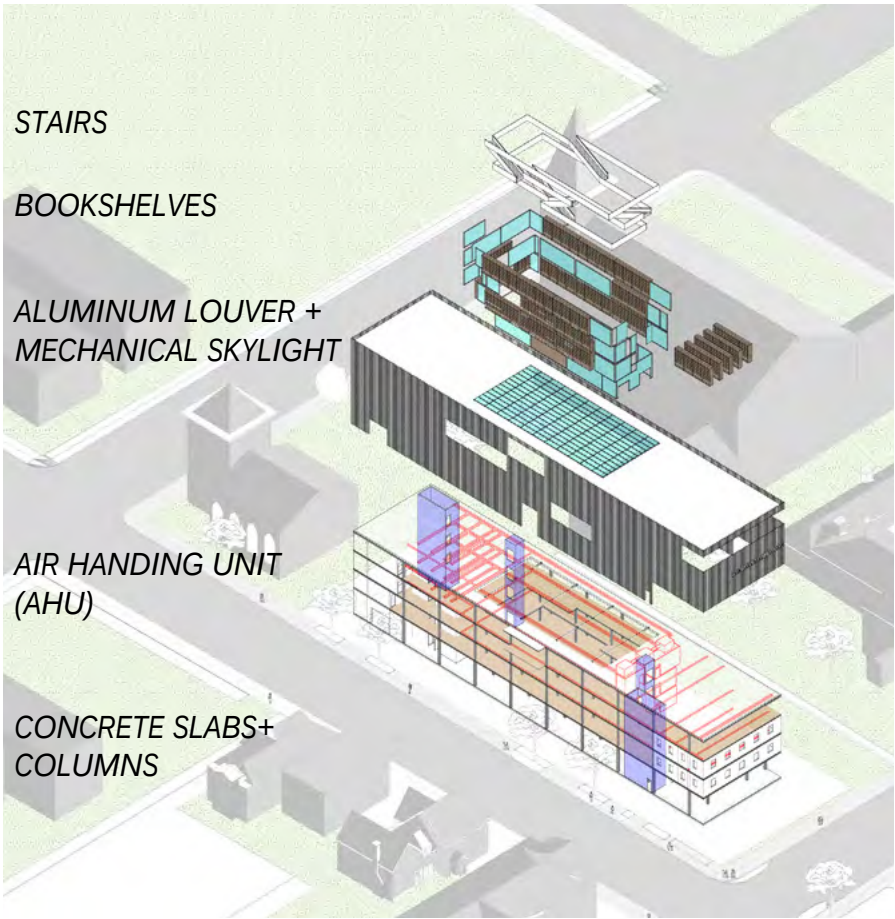


Structural + Mechanical axon

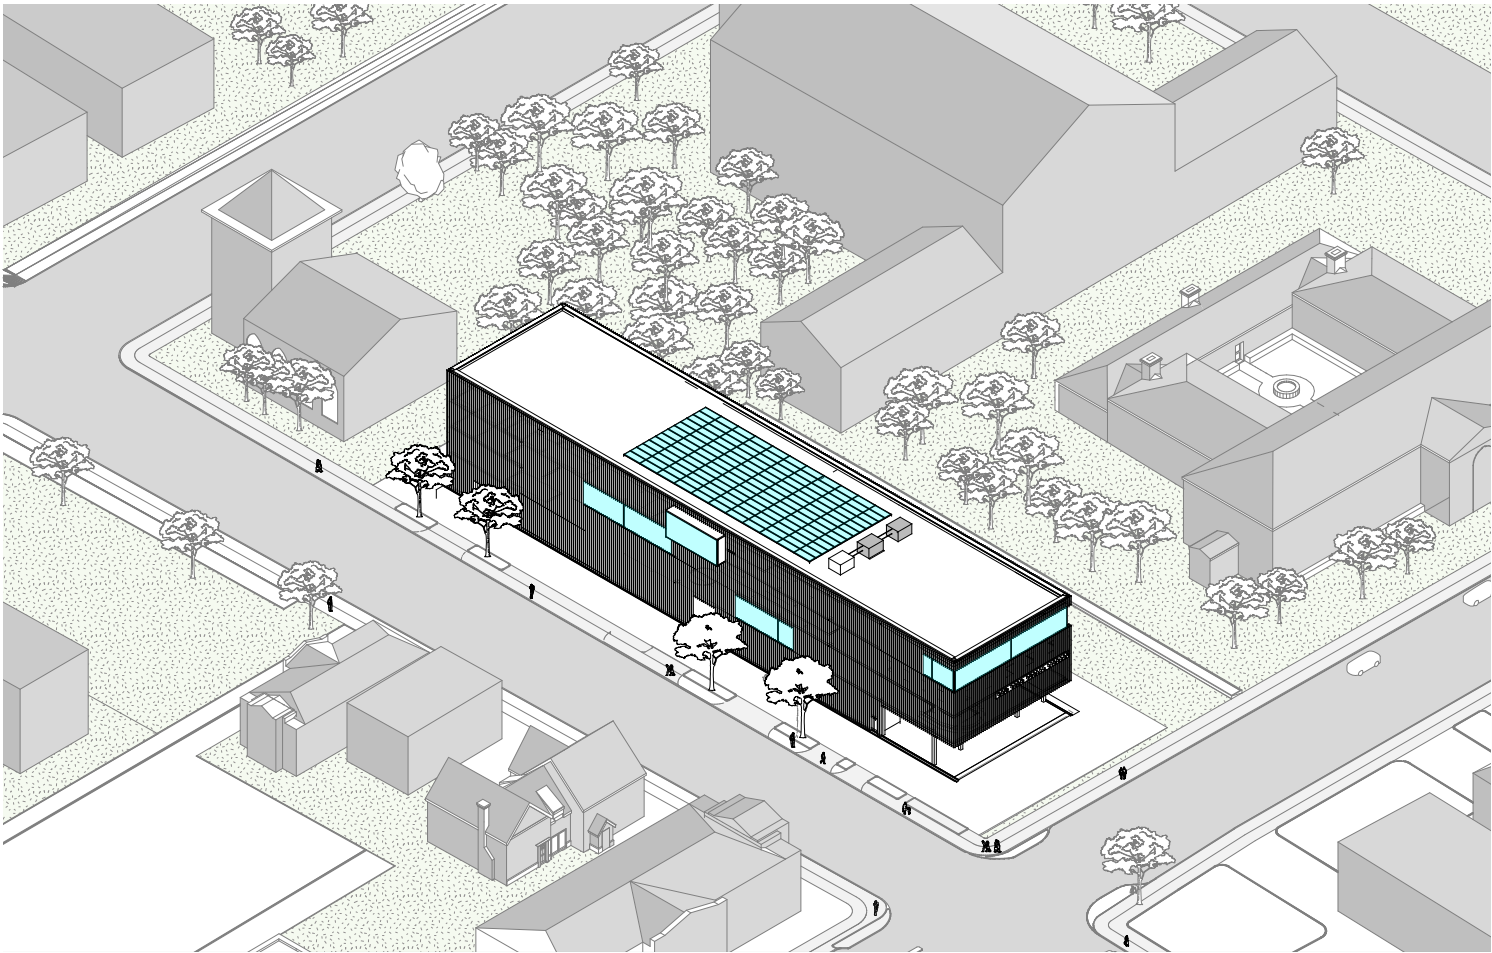


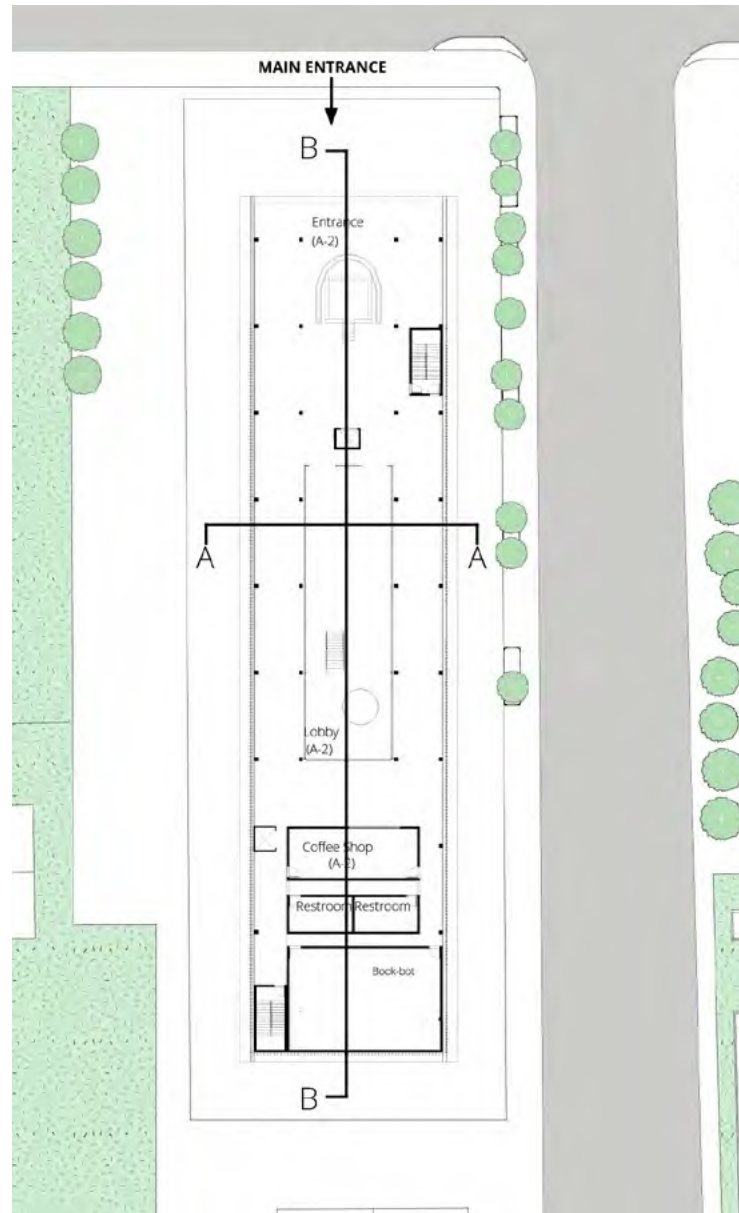


First Floor Plan
Scale: 1/64" = 1'-0"

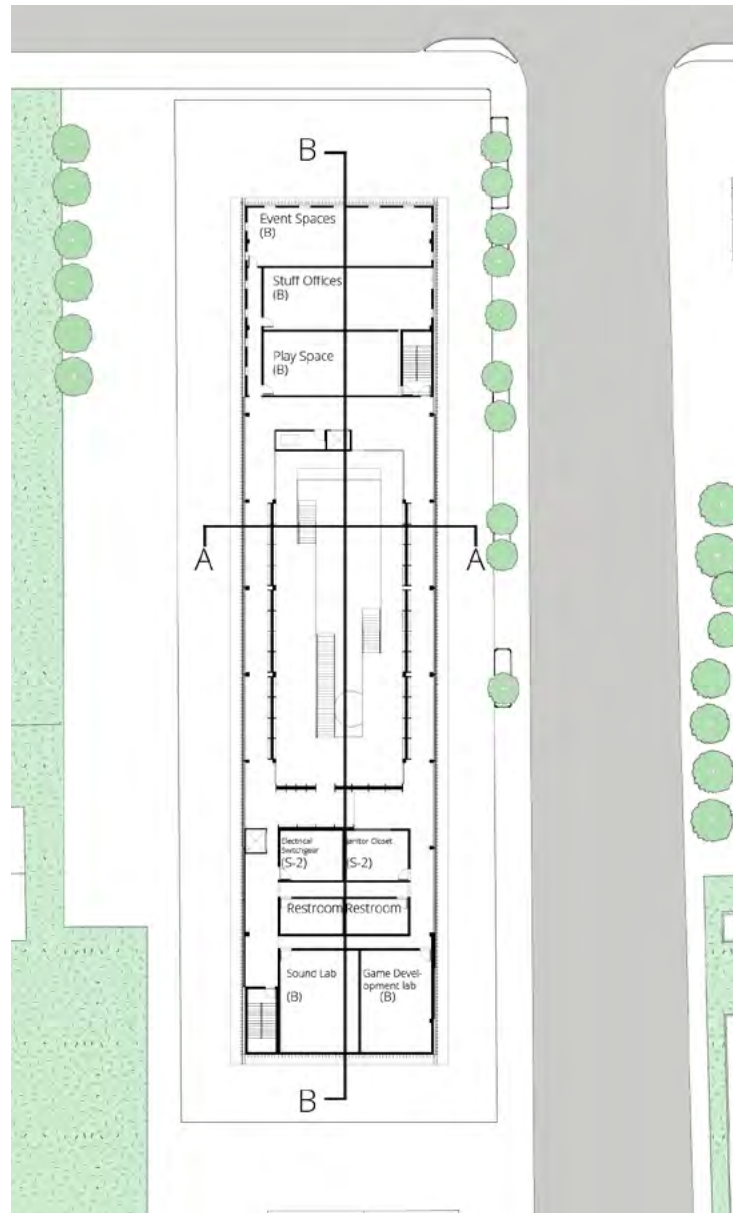

Second Floor Plan

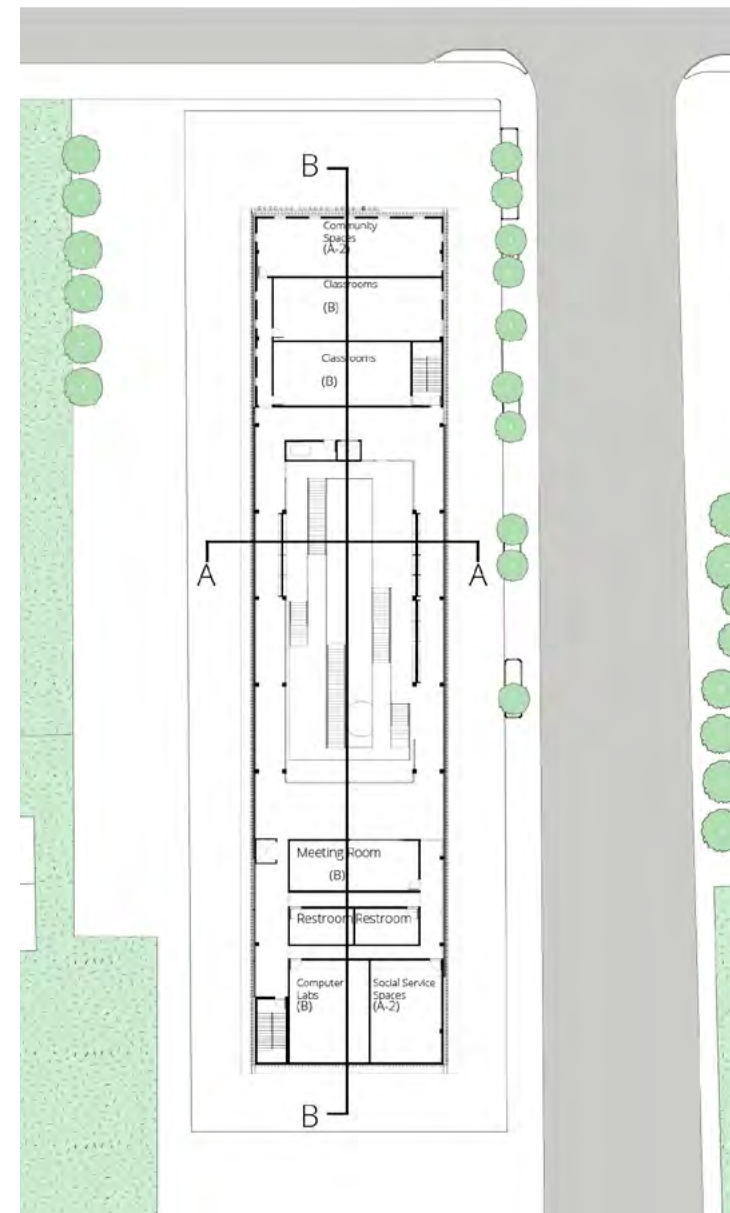

Third Floor Plan

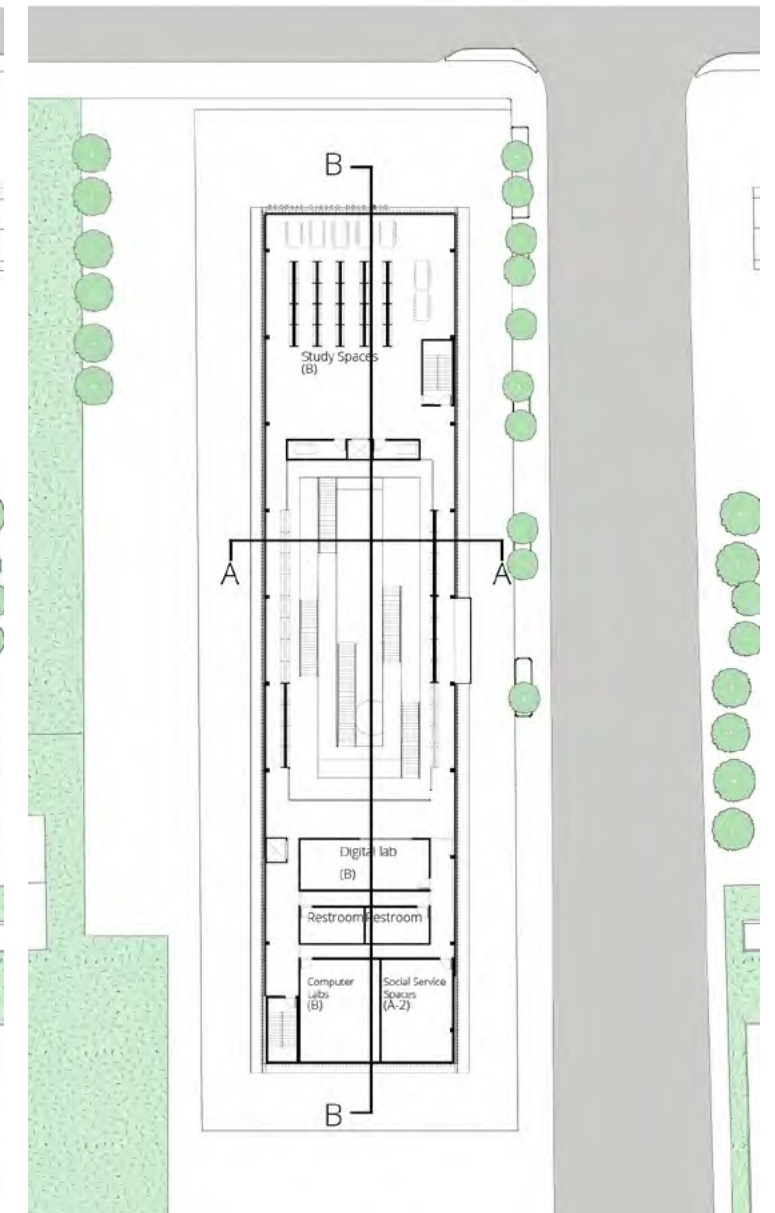

Fourth Floor Plan



North Elevation
Scale: 1/64" = 1'-0"



East Elevation



SECTION A-A



SECTION B-B

